




OUTBOARD PROFILE

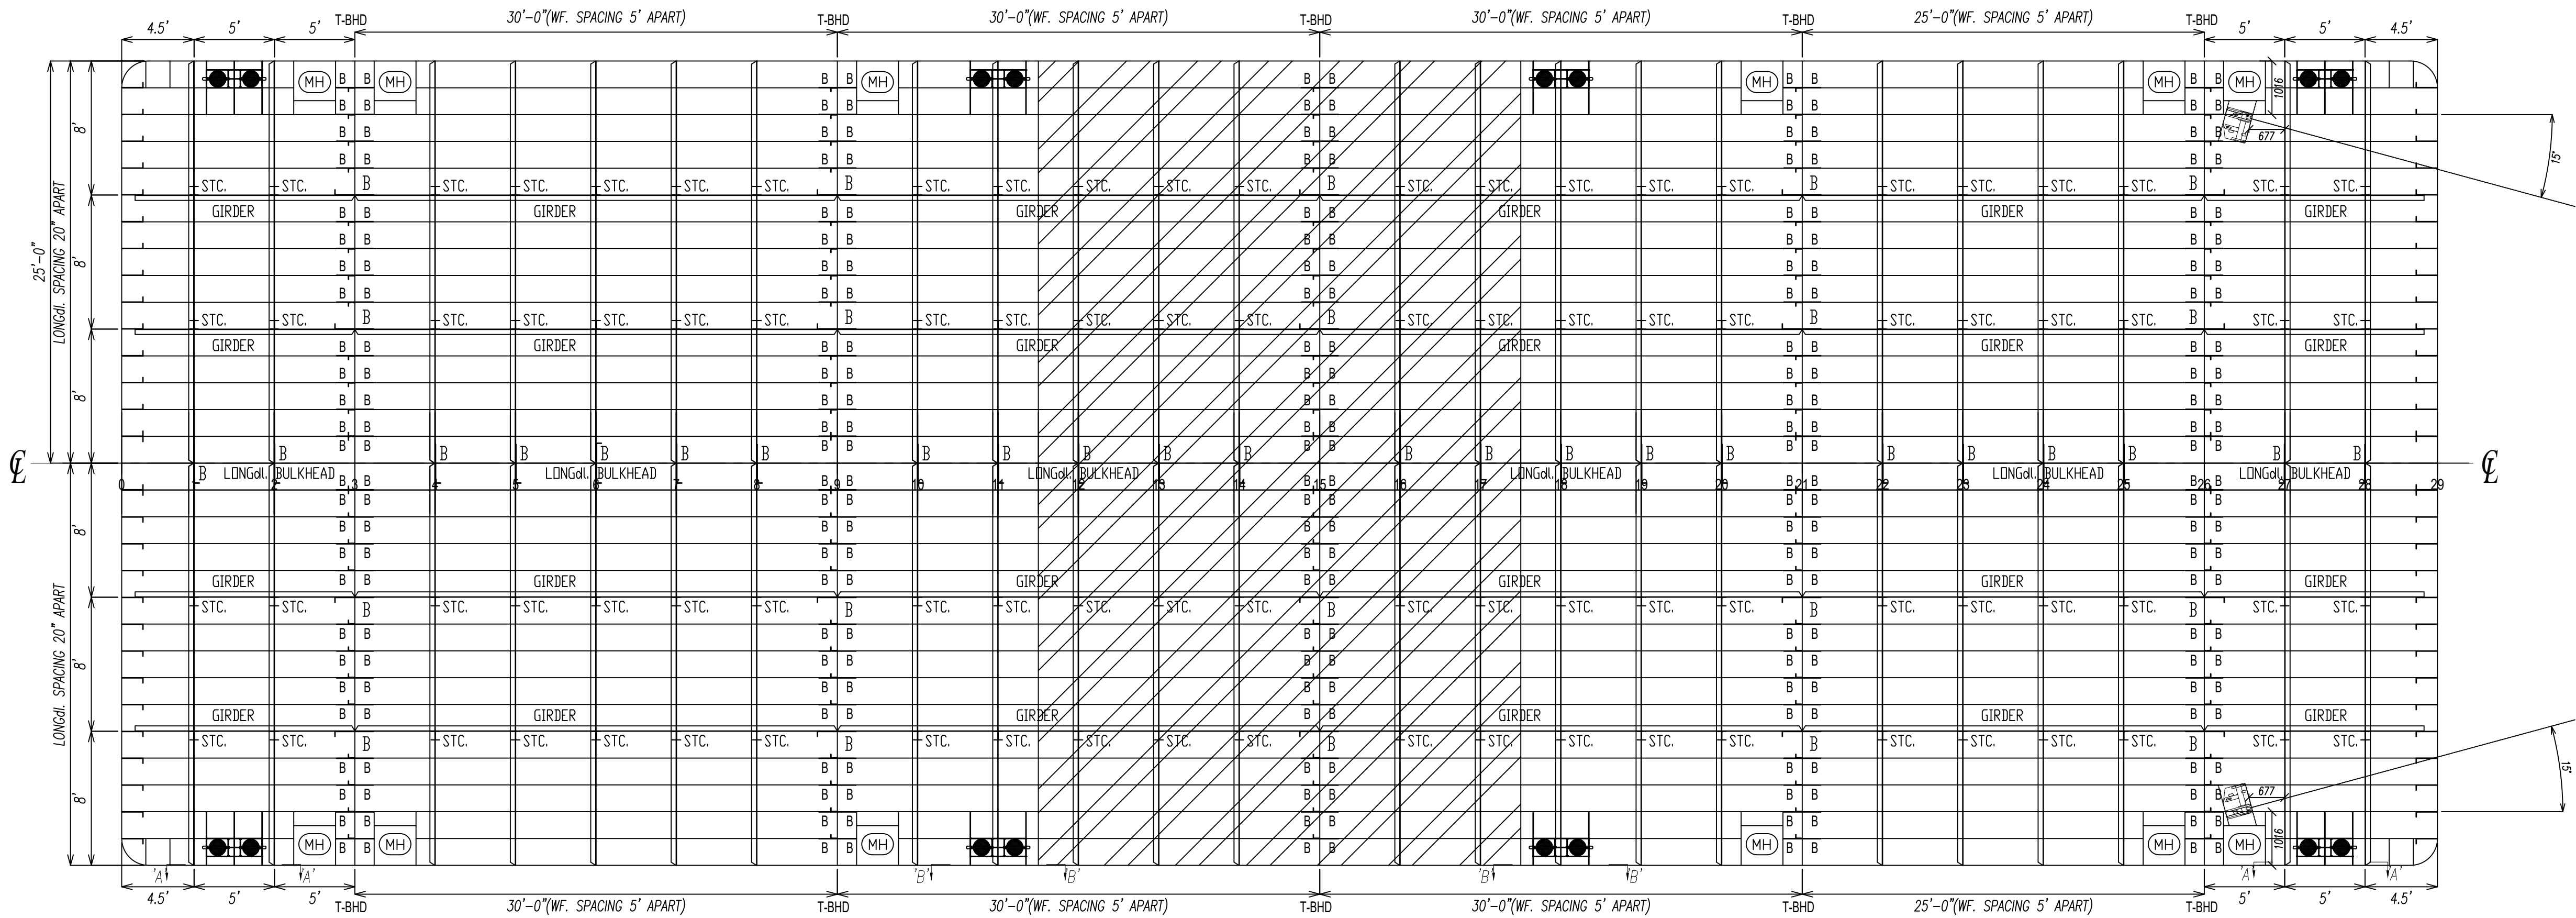


DECK PLAN

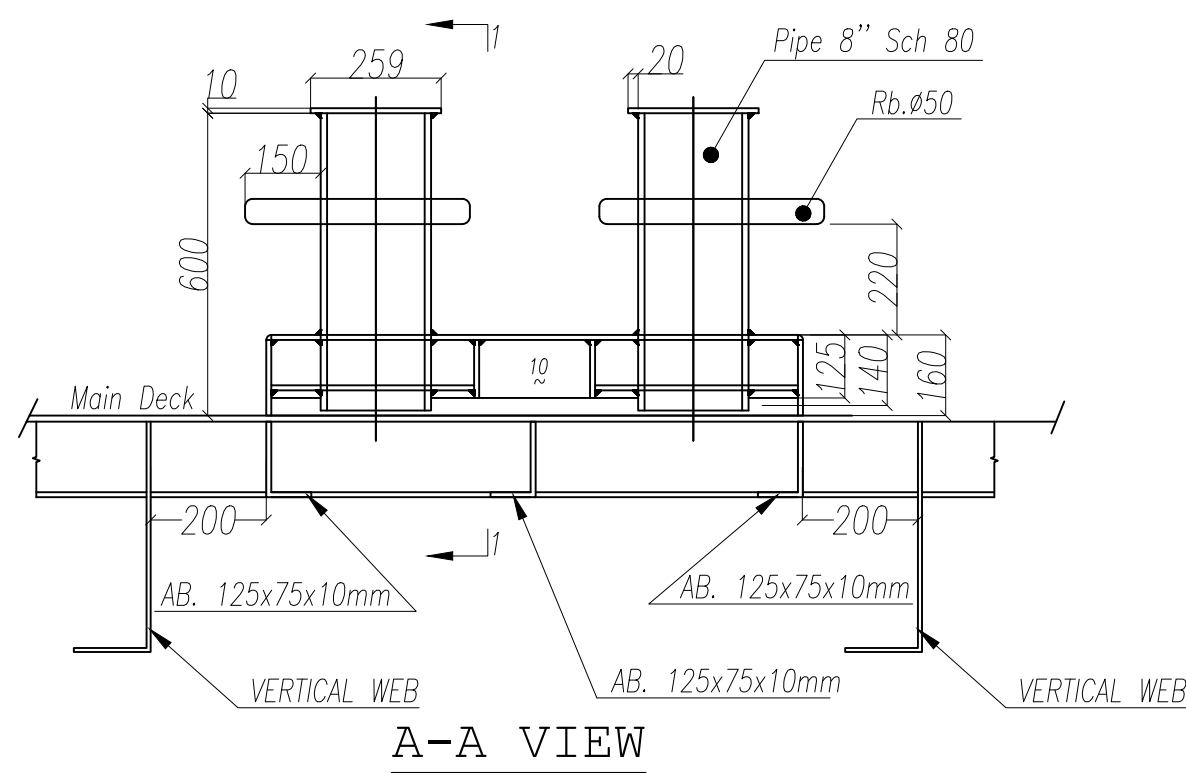

A-A VIEW

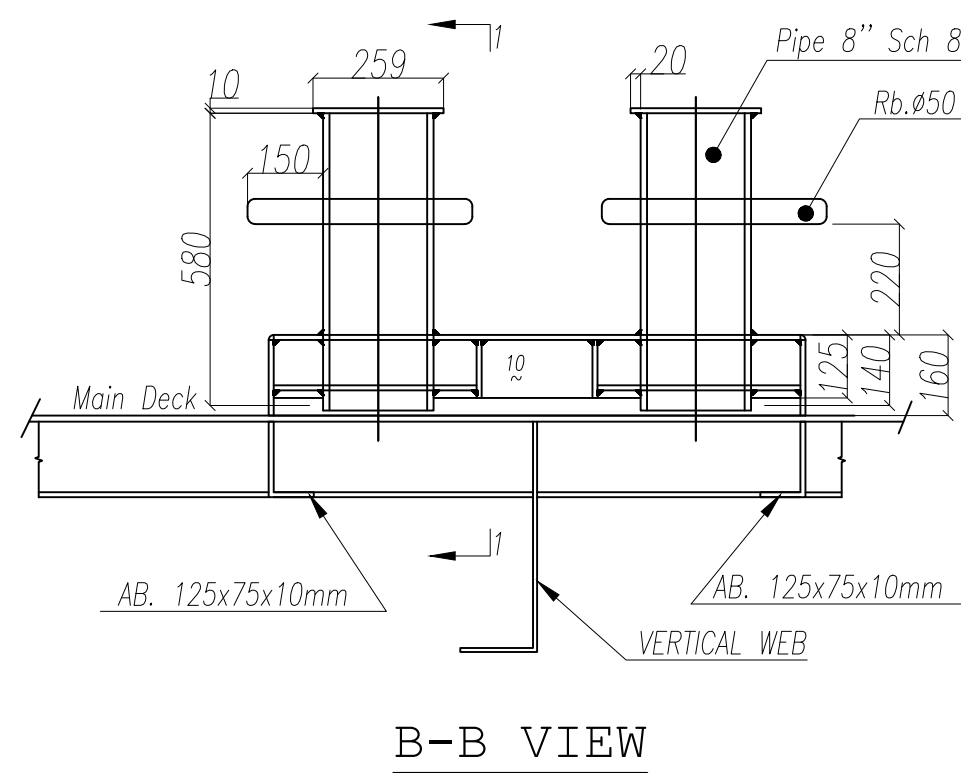


B-B VIEW

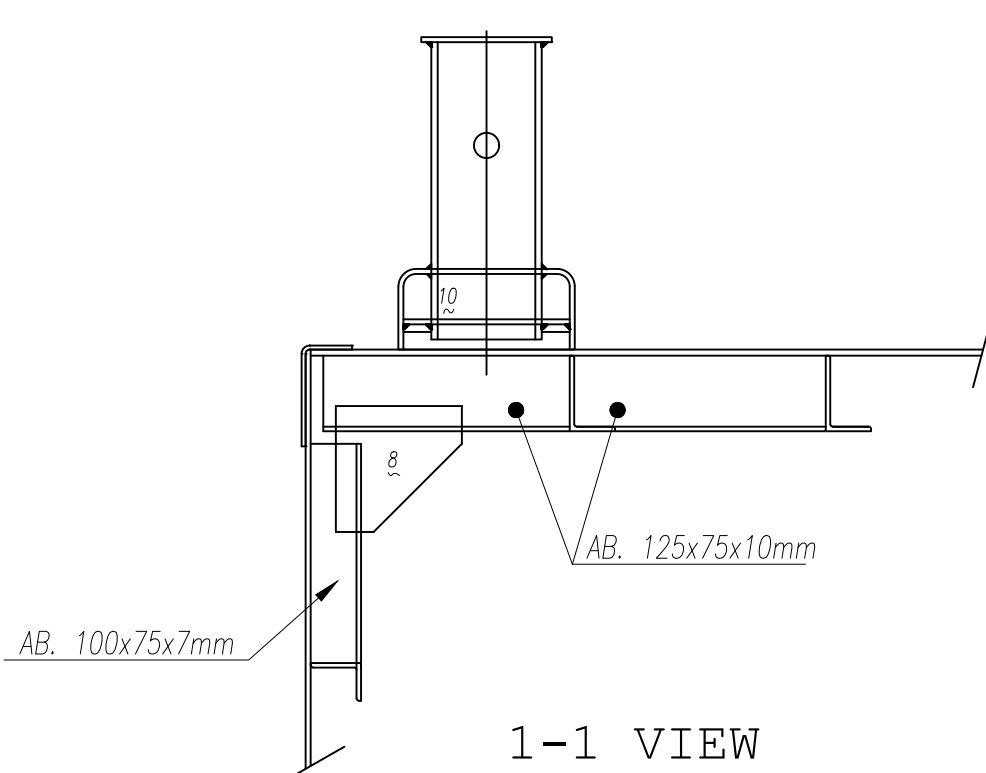

1-1 VIEW

DOUBLE BOLLARD
8 PCS (P/S) SWL 20 T

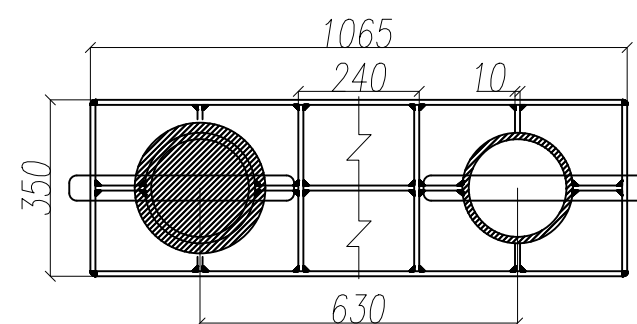

PLAN VIEW

ITEM	MODIFICATION	BY	DATE
OWNER			
BUILDER			
PROJECT	FLOATING BARGE 144'X50'X10'		
TITLE	BOLLARD ARRANGEMENT & DETAIL		
PREPARED	CHECKED	APPROVED	CLASS: BKI
KKH	AR	AR	HULL NO: H560
09/07/2026	09/07/2026	09/07/2026	SCALE: 1:75
SISTER SHIP: -			REV: 0
			A1-STD

THIS DOCUMENT AND THE INFORMATION IT CONTAINS IS
COPYRIGHT AND REMAINS THE PROPERTY OF PT BANGSAR ABADI.
THE DESIGN IS NOT TO BE COPIED IN WHOLE OR IN PART OR
DISCLOSED TO ANY THIRD PARTY FOR ANY PURPOSE WITHOUT
PRIOR PERMISSION IN WRITING.