


OUTBOARD PROFILE

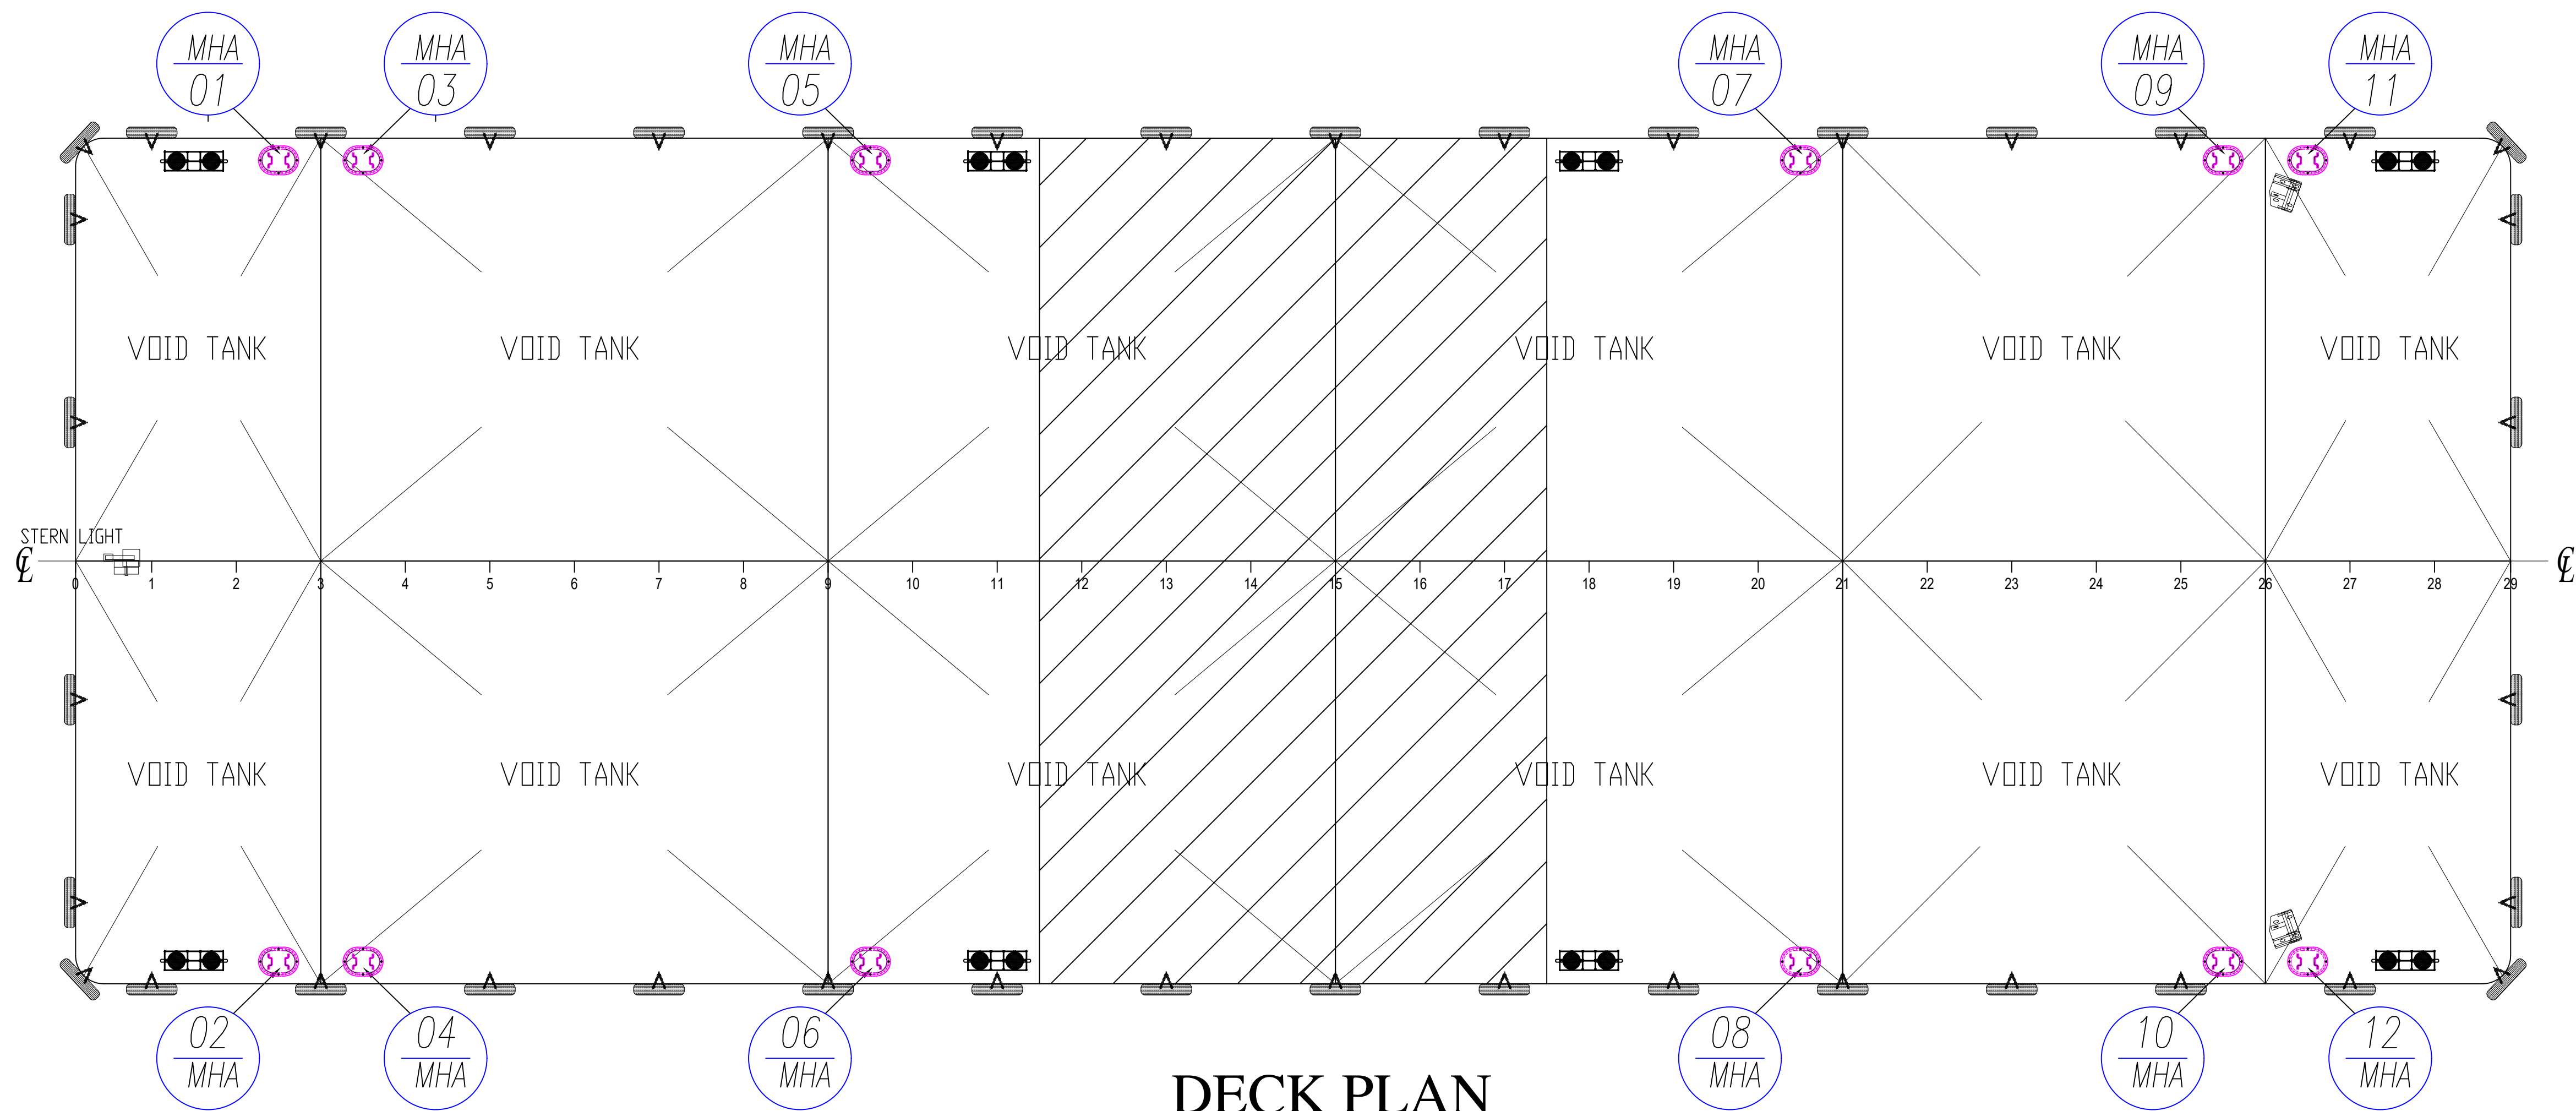


DECK PLAN


DETAIL COVER MANHOLE

SCALE 1:8


MANHOLE 600x400
TYPE "A"

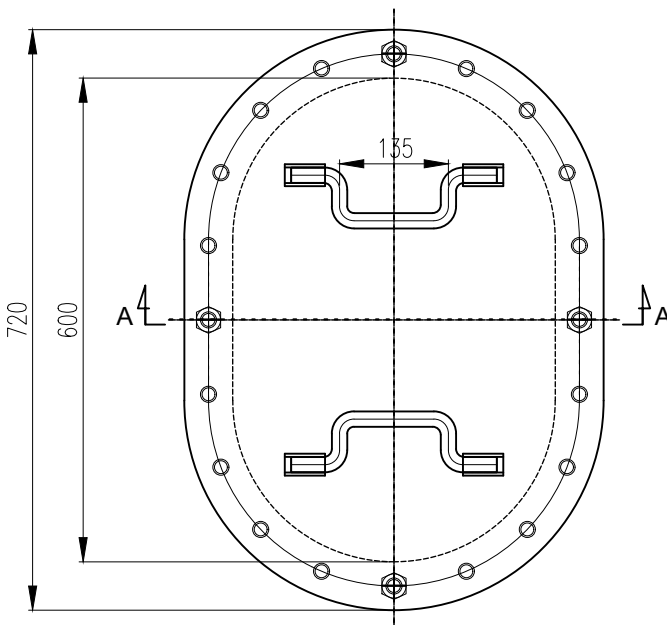


HANDLE DETAIL A
1:20

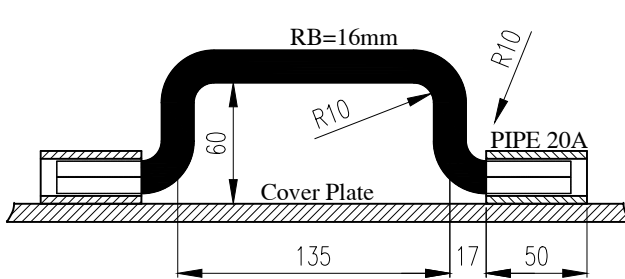

SECTION A-A
1:8

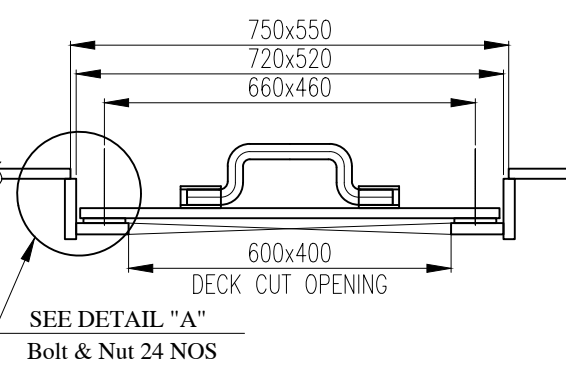

DETAIL A
1:32

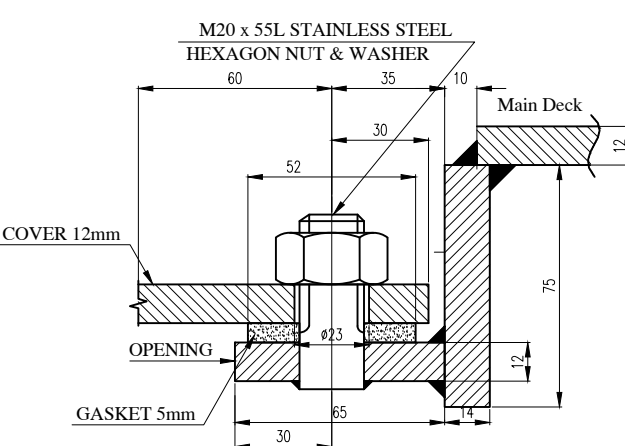

THIS DOCUMENT AND THE INFORMATION IT CONTAINS IS
COPYRIGHT AND REMAINS THE PROPERTY OF PT BANGKAR ABADI.
THE DESIGN IS NOT TO BE COPIED IN WHOLE OR IN PART OR
DISCLOSED TO ANY THIRD PARTY FOR ANY PURPOSE WITHOUT
PRIOR PERMISSION IN WRITING.

ITEM	MODIFICATION	BY	DATE	
OWNER				
BUILDER				
PROJECT				
FLOATING BARGE 144'X50'X10'				
TITLE				
MANHOLE ARRANGEMENT & DETAILS				
PREPARED	CHECKED	APPROVED	CLASS: BK1	DWG NO: BA26-FB56010-07
KKH	AR	AR	HULL NO: H560	SCALE: 1:75
09/07/2026	09/07/2026	09/07/2026	SHEET: 01 OF 01	REV: 0
SISTER SHIP: -				A1-STD