




ELEVATION
(OUT-SIDE)

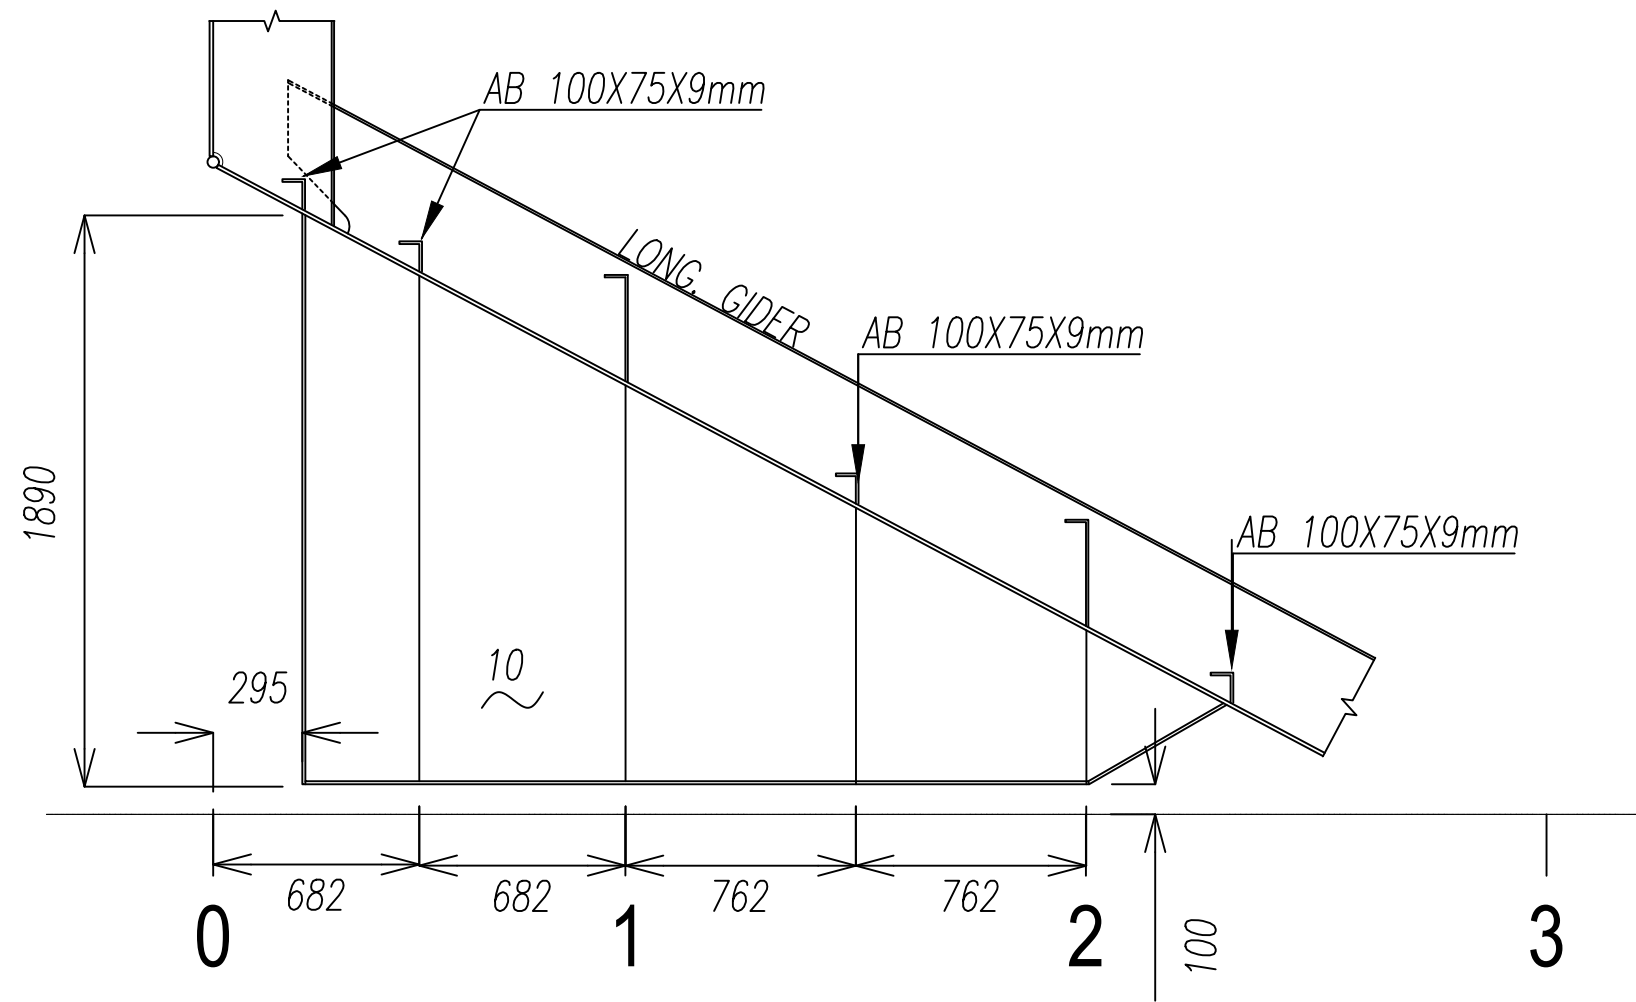


ELEVATION
(IN-SIDE)

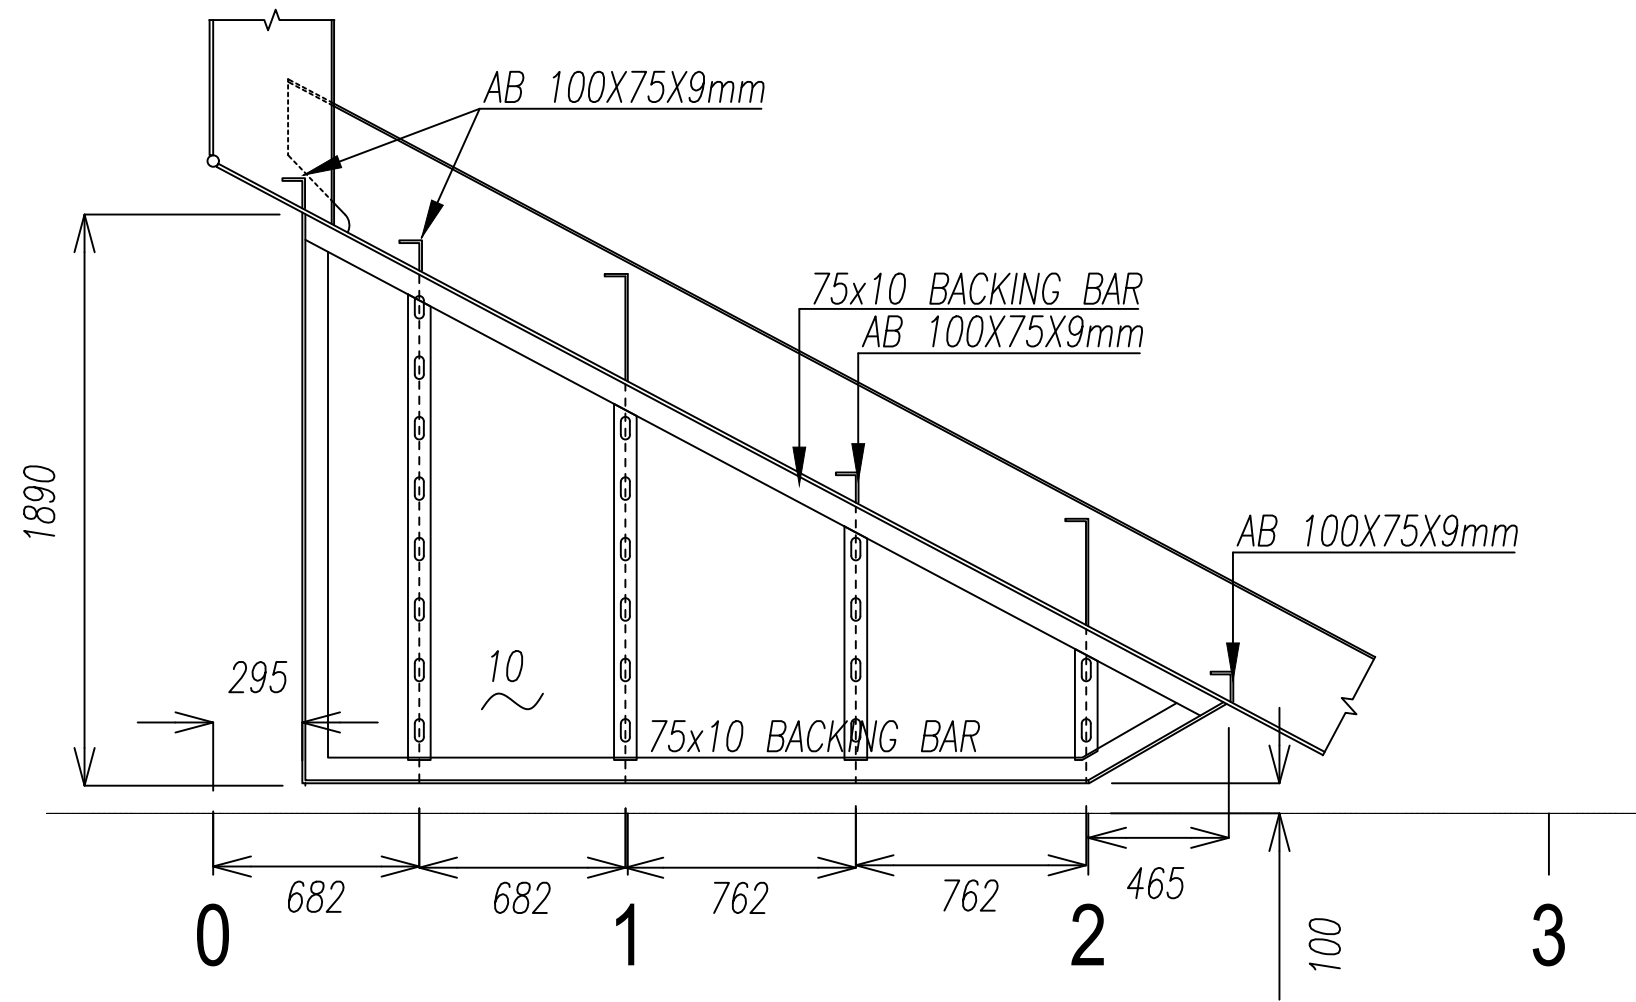


SLOT WELD DTL
1:2

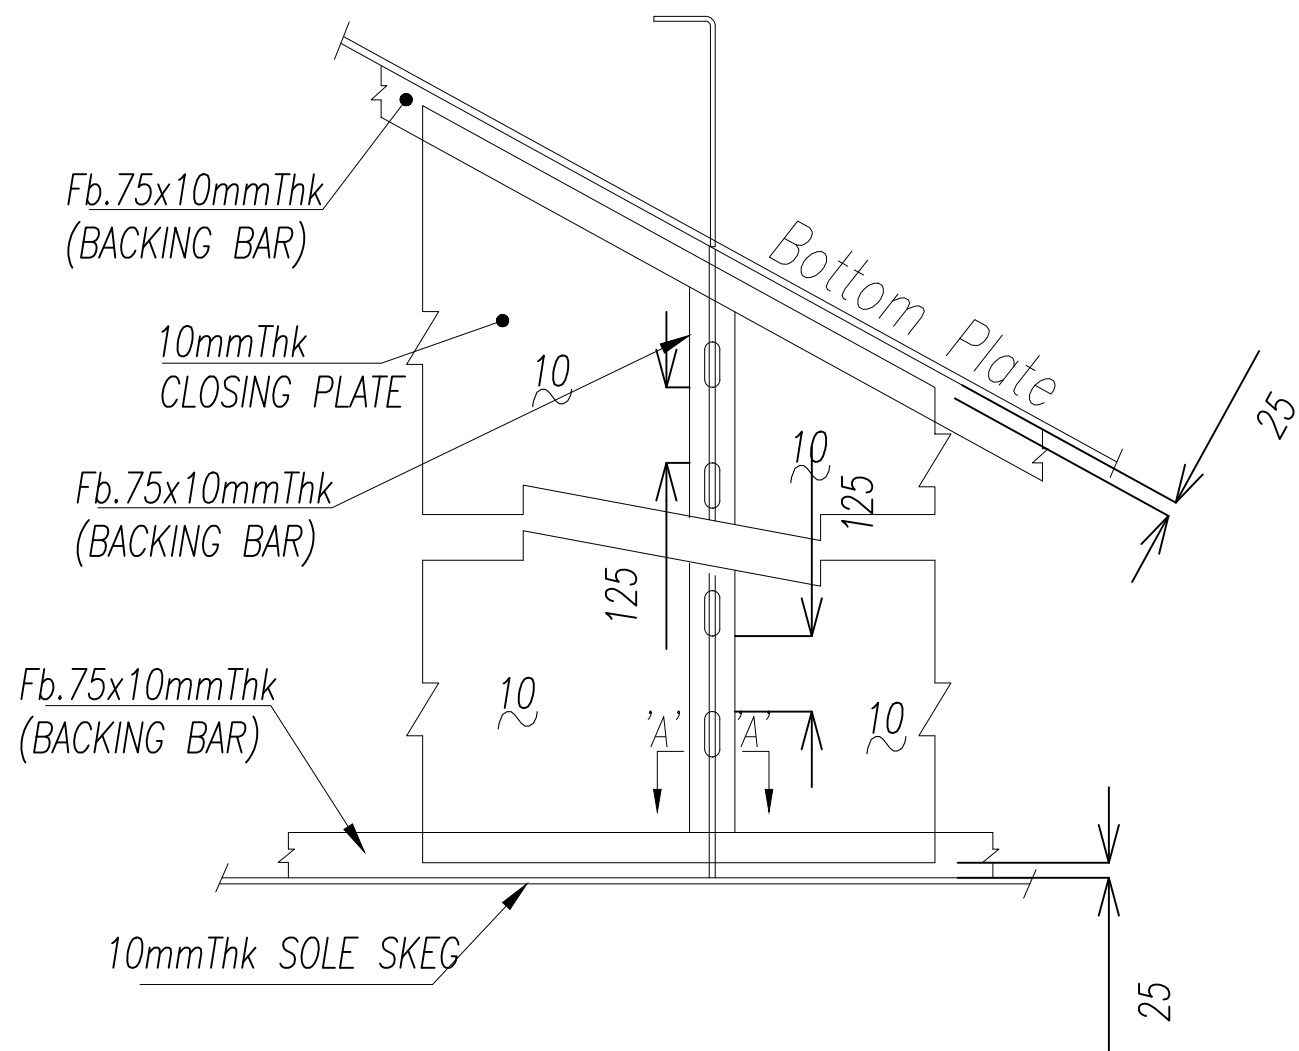


SECTION 'A-A'
1:10

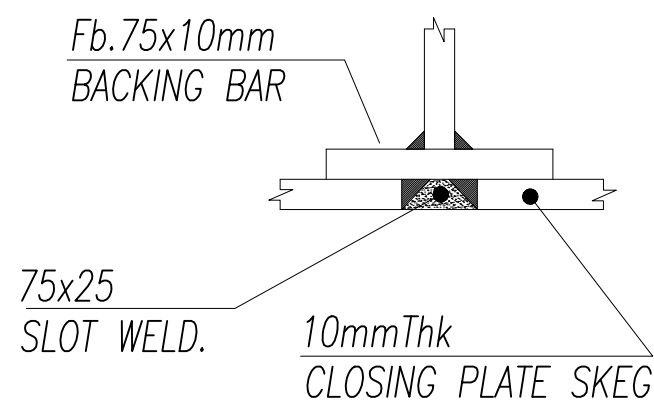


PLAN VIEW
STBD SHOWN, PORT SIMILAR

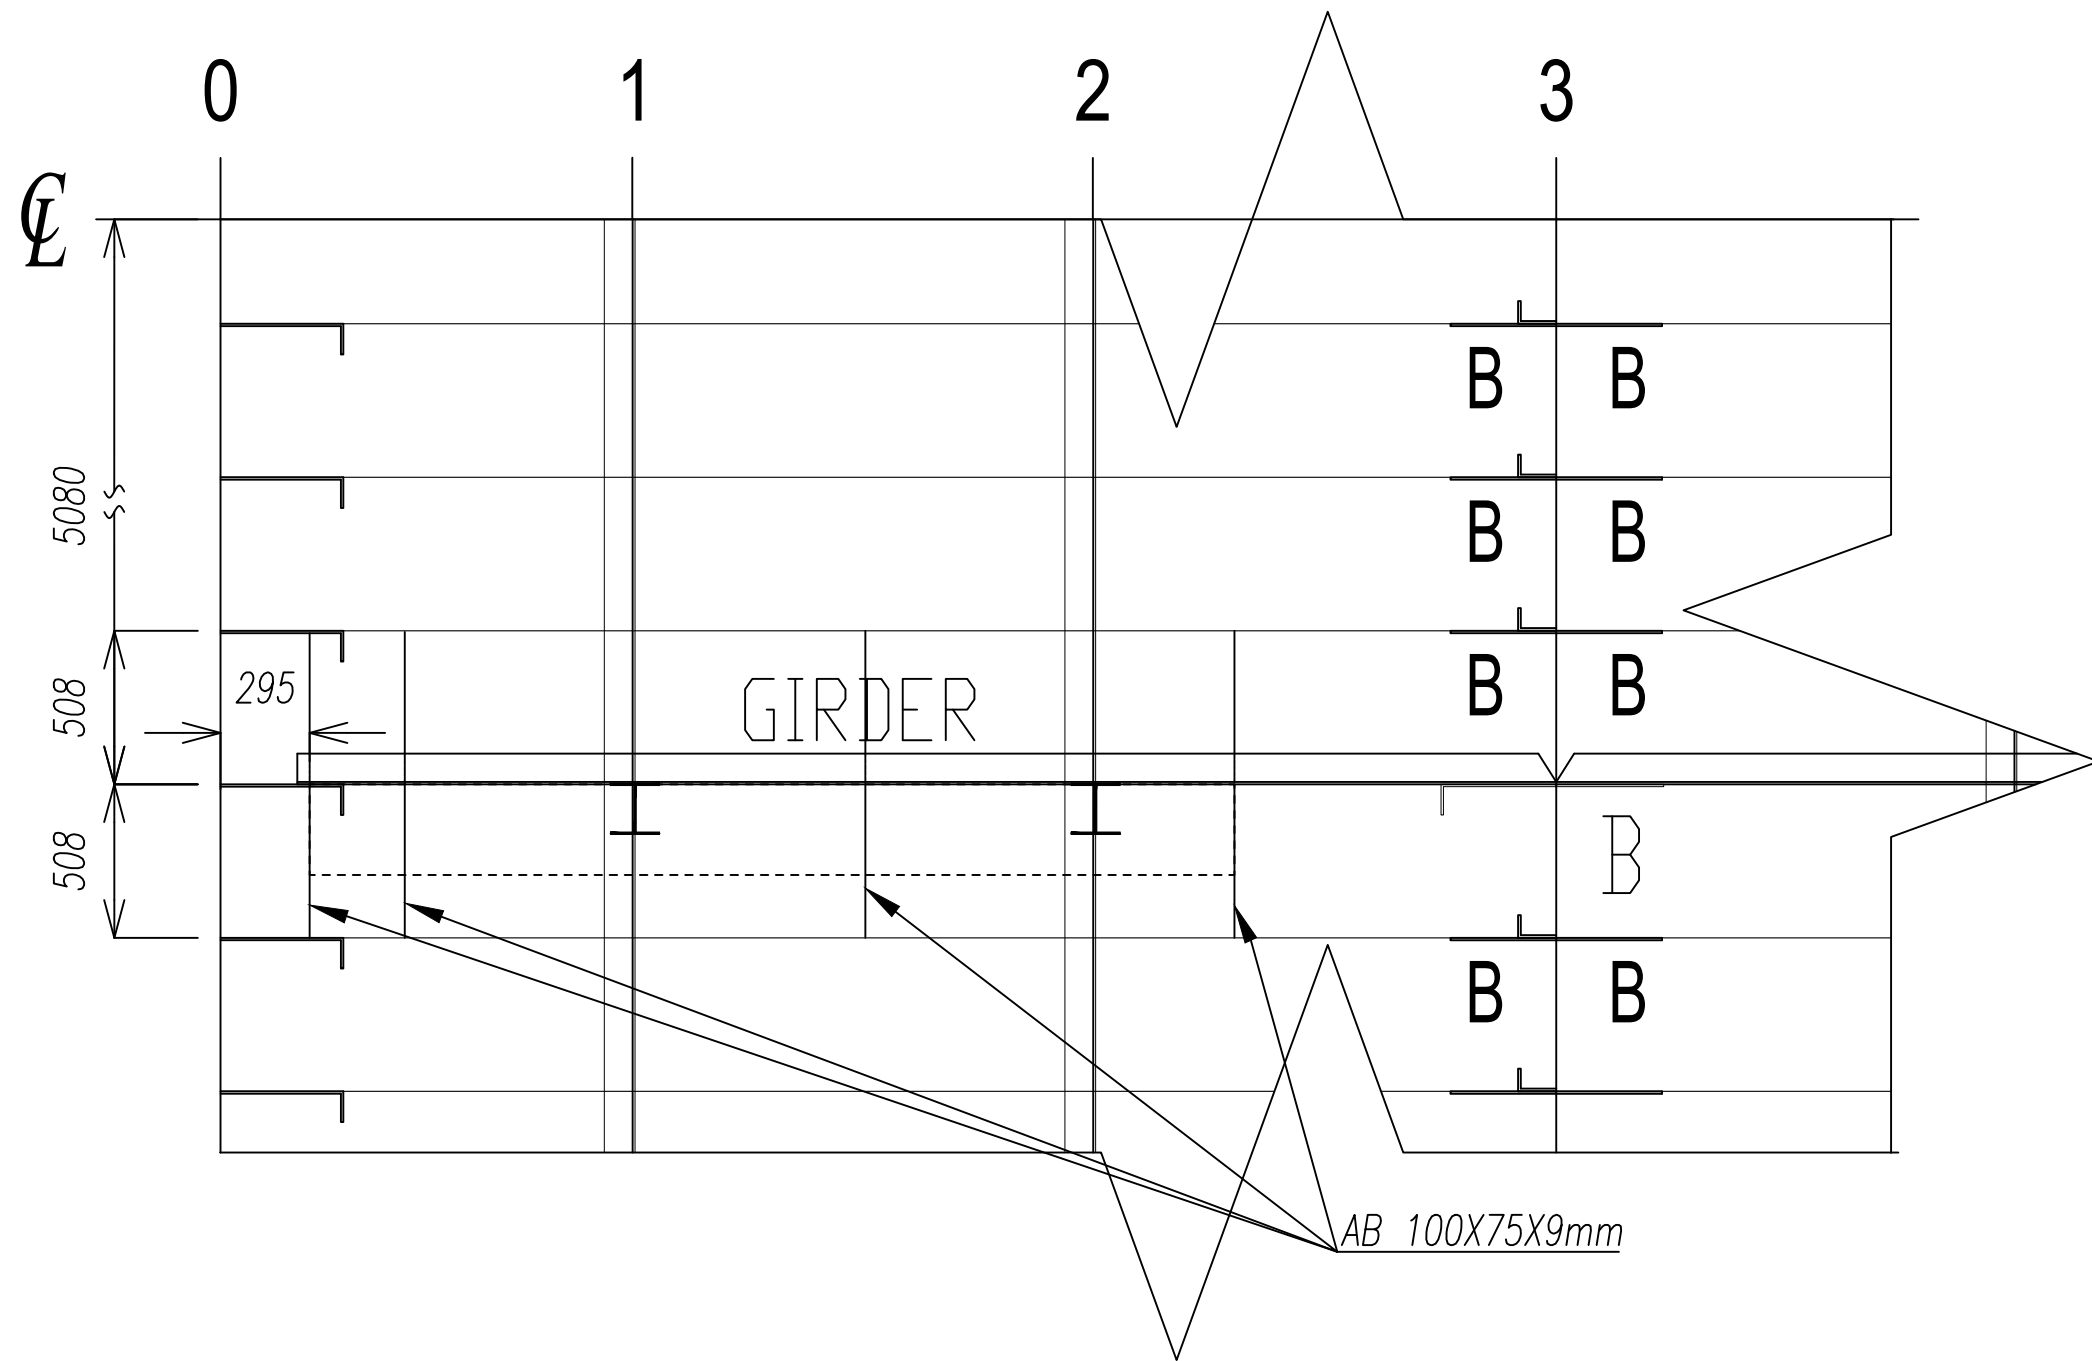


FRAME 0 +682

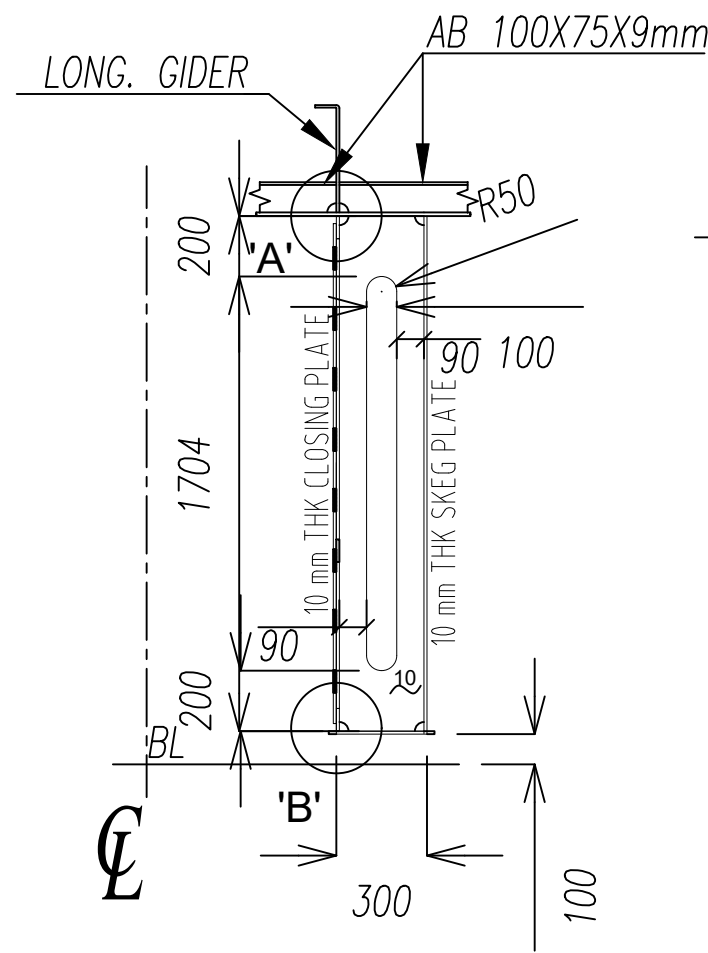


FRAME 1

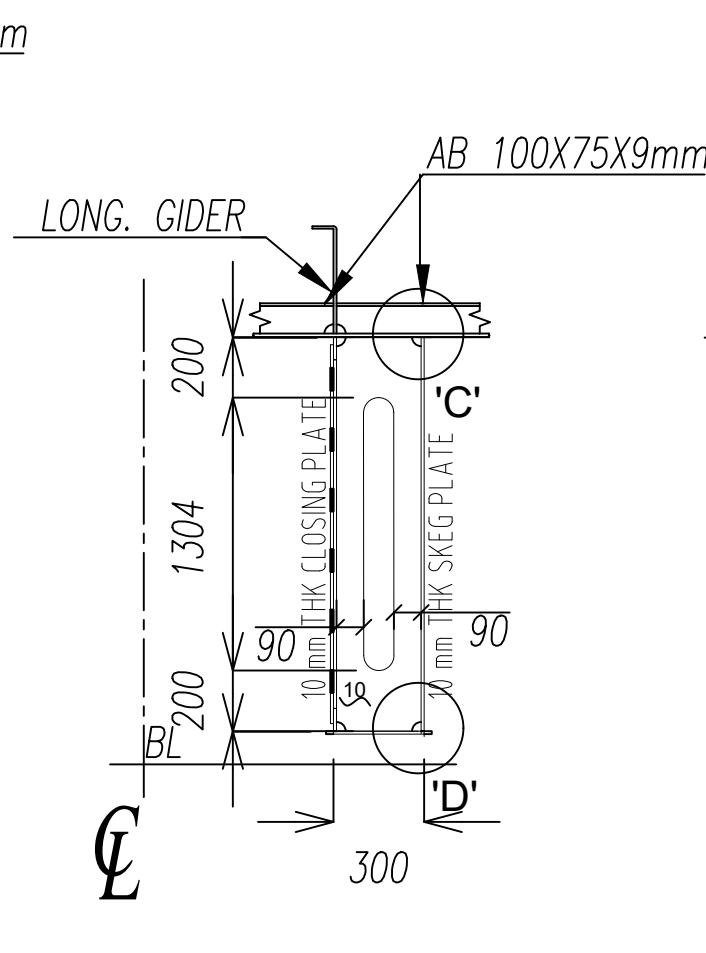


FRAME 1 +762

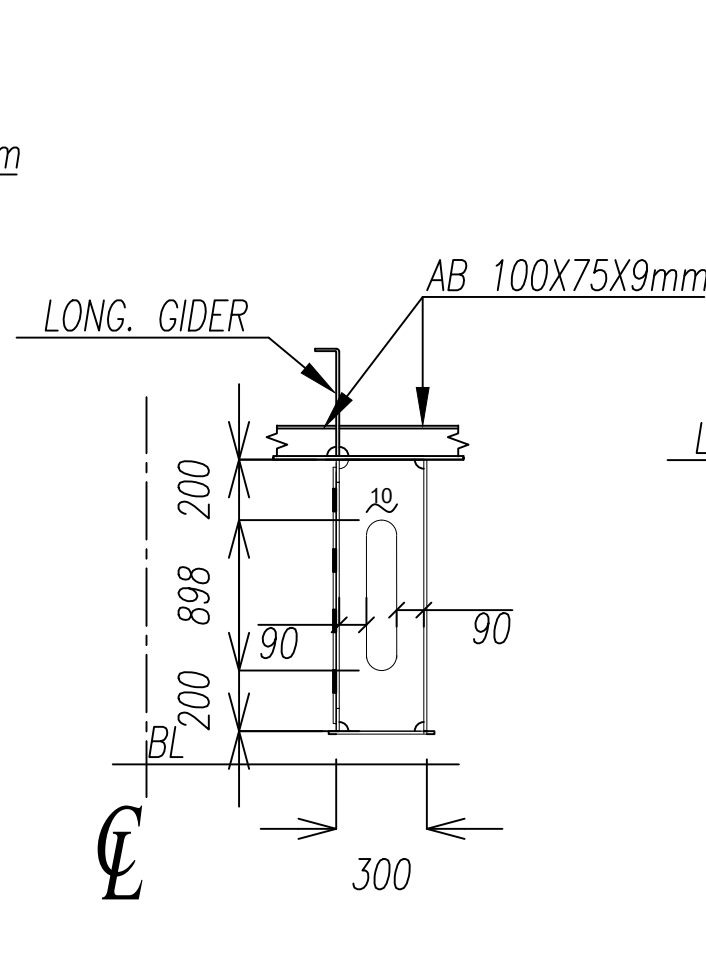


FRAME 2

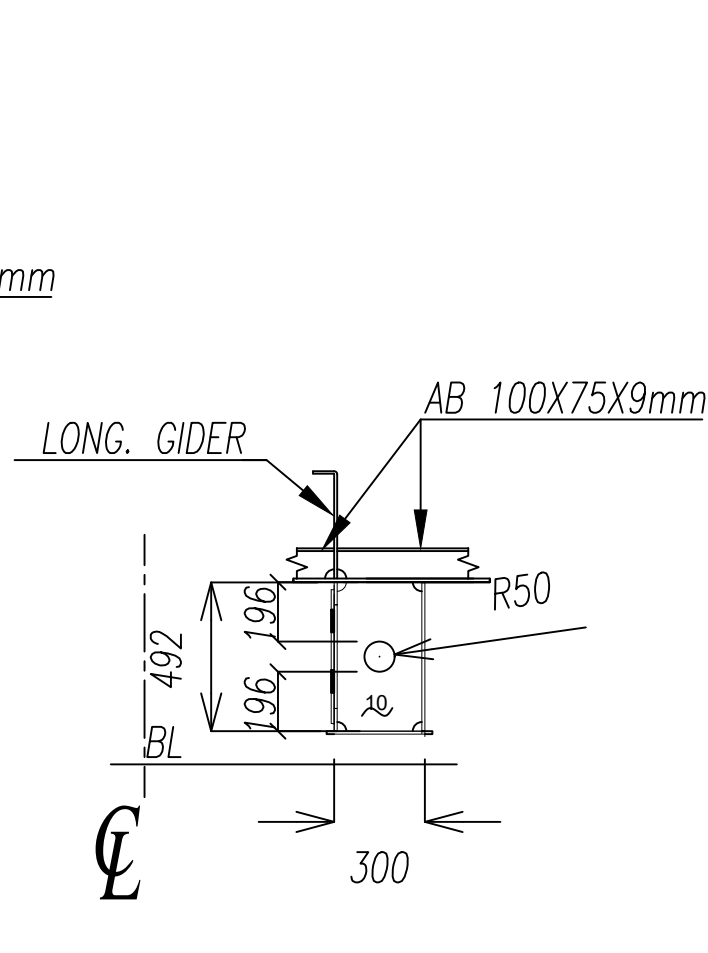


DTL. A

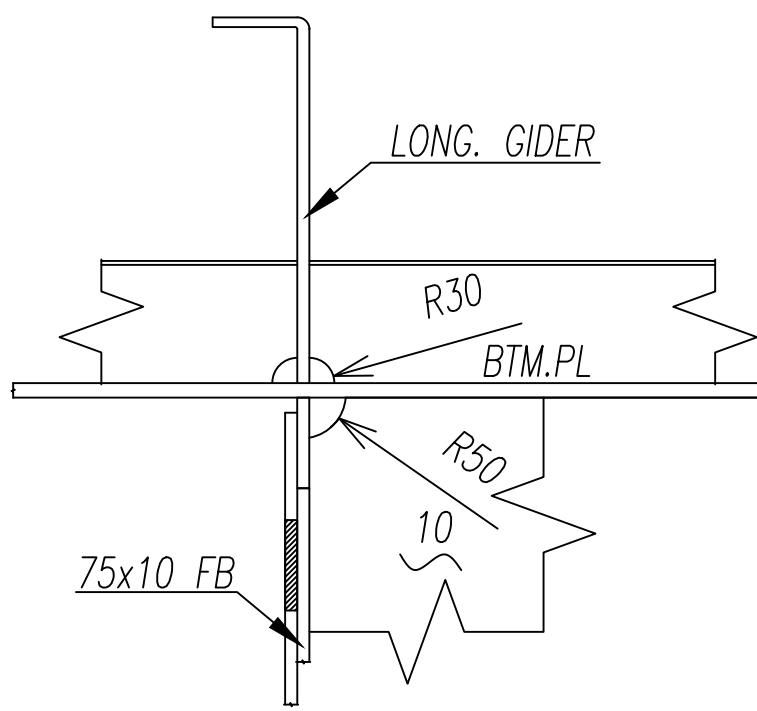


DTL. B

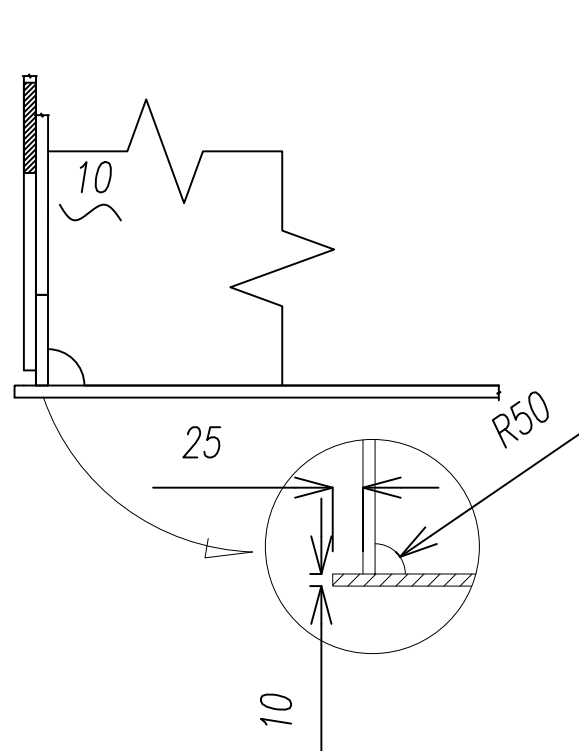

DTL. C

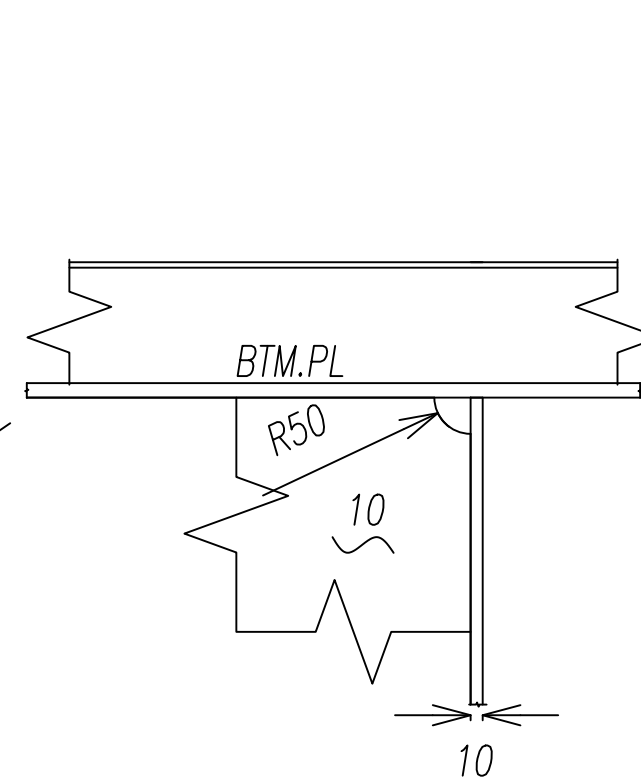

DTL. D

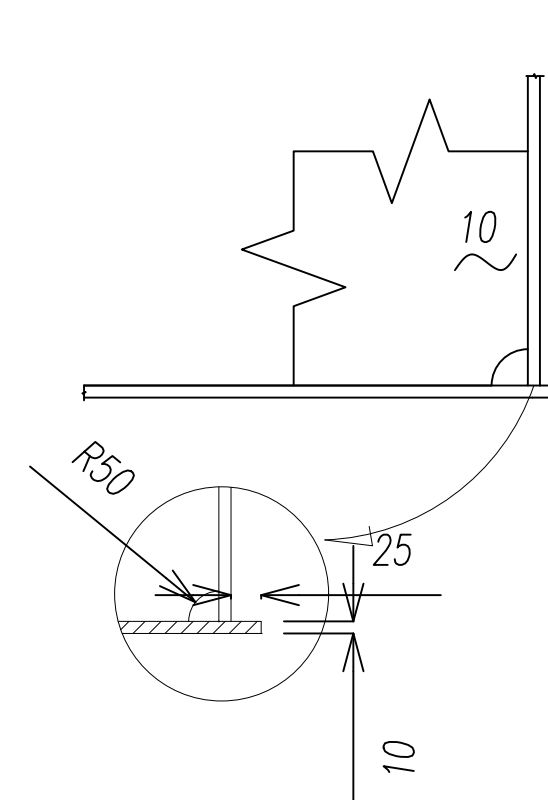

NOTES
1. ALL WELDING SLOT ON THE SKEG SHALL BE GRINDING SMOOTH

ITEM	MODIFICATION	BY	DATE
OWNER			
BUILDER			
PROJECT	FLOATING BARGE 144'X50'X10'		
TITLE	SKEG CONSTRUCTION		
PREPARED	CHECKED	APPROVED	CLASS: BK1
KKH	AR	AR	SCALE: 1:25
09/07/2026	09/07/2026	09/07/2026	SHEET: 01 OF 01
SISTER SHIP : -			REV: 0

THIS DOCUMENT AND THE INFORMATION IT CONTAINS IS
COPYRIGHT AND REMAINS THE PROPERTY OF PT BANGSAR ABADI.
THE DESIGN IS NOT TO BE COPIED IN WHOLE OR IN PART OR
DISCLOSED TO ANY THIRD PARTY FOR ANY PURPOSE WITHOUT
PRIOR PERMISSION IN WRITING.