



OUTBOARD PROFILE

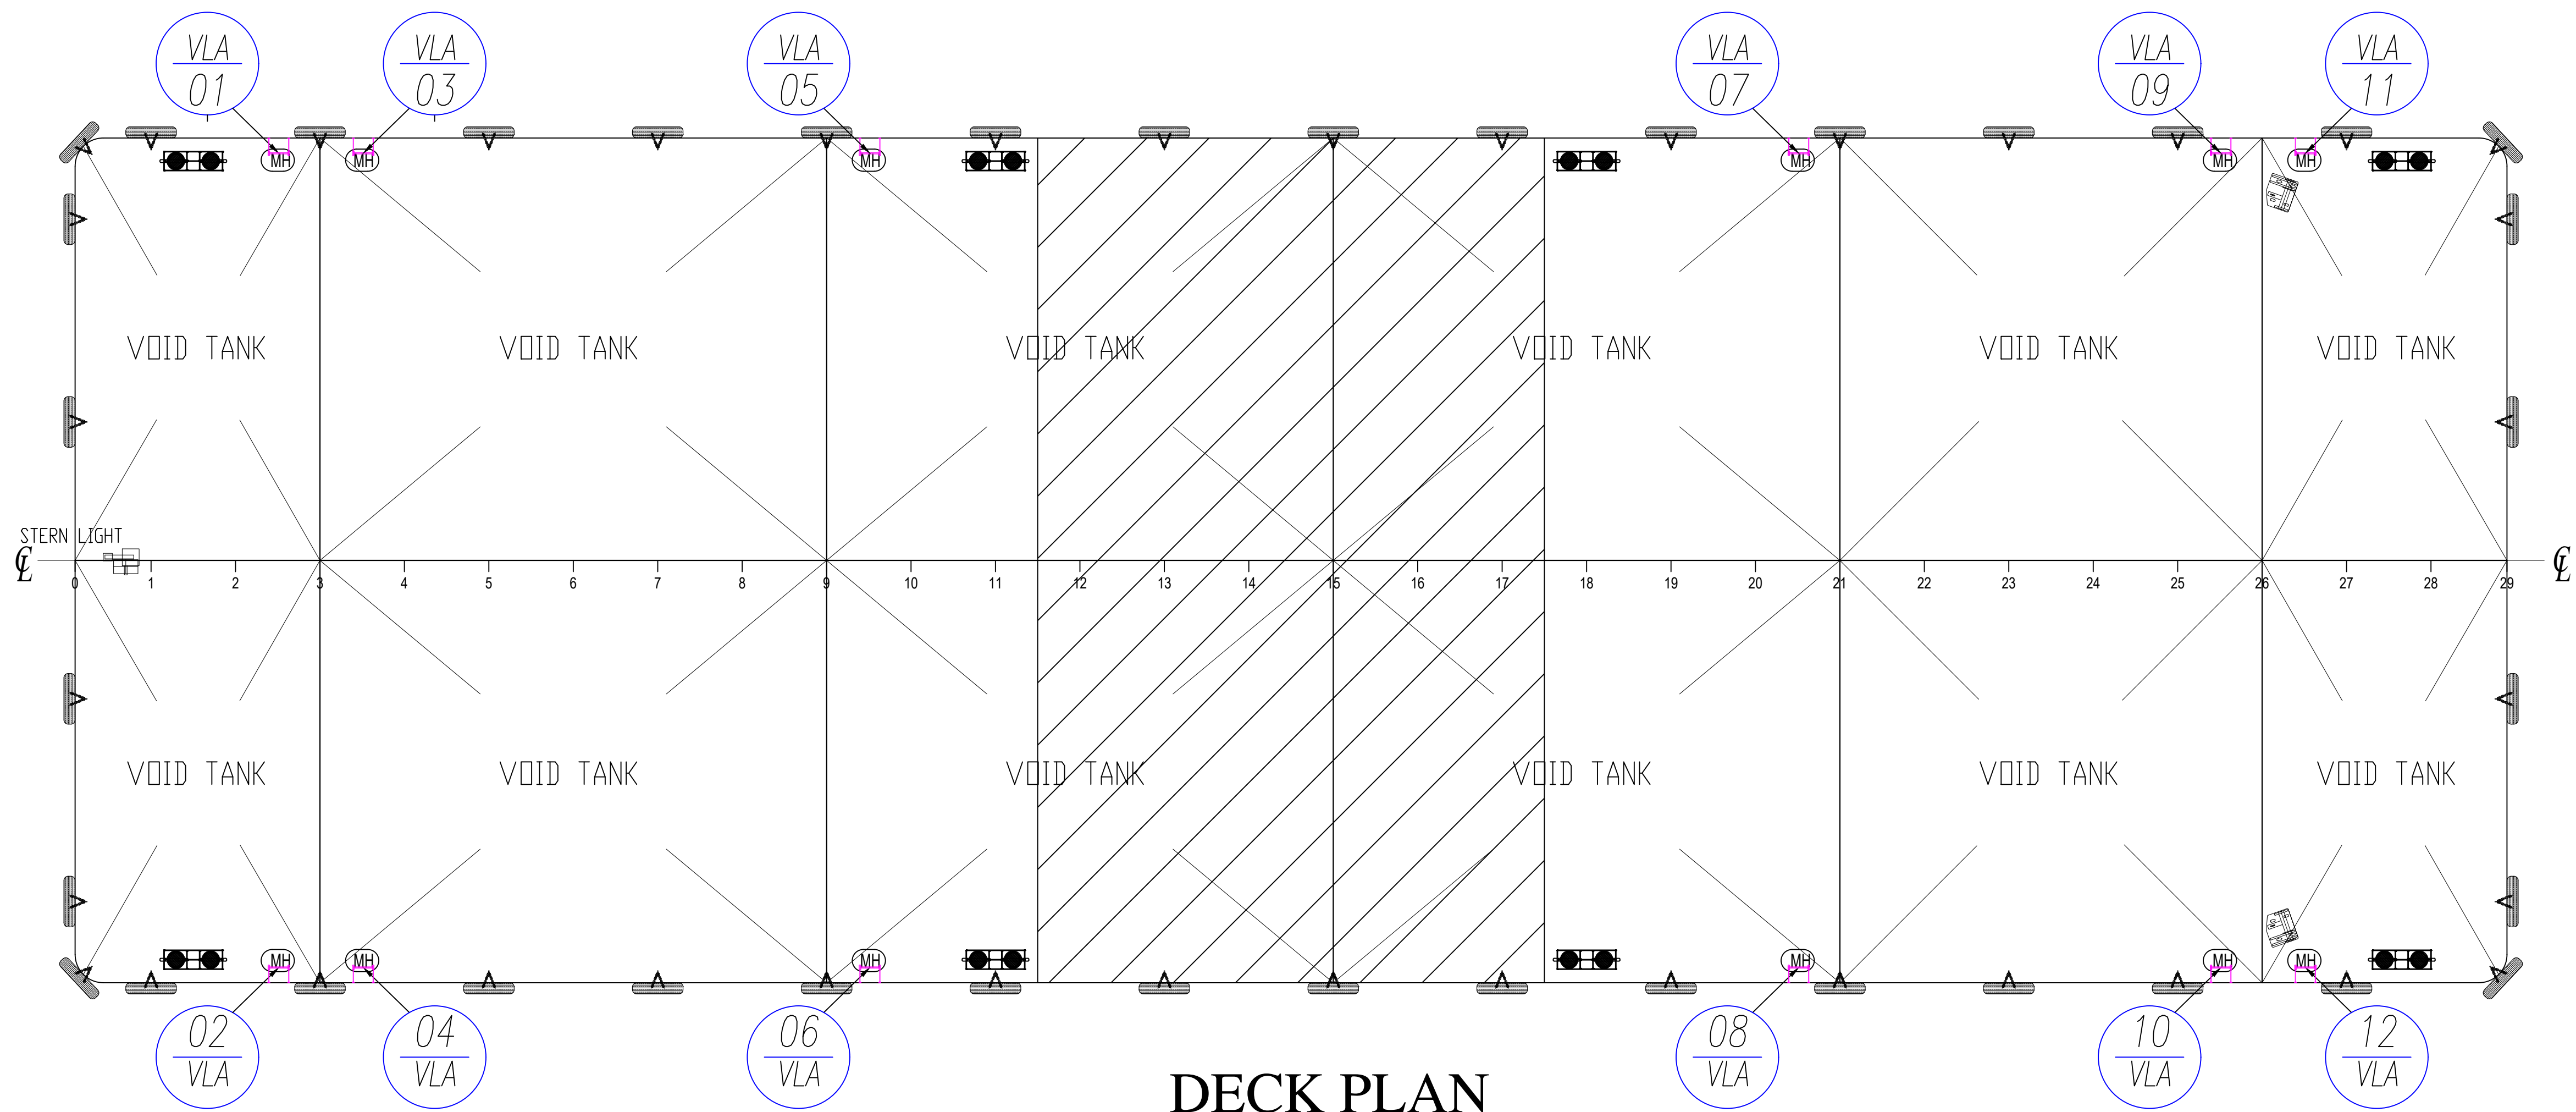


DECK PLAN

DETAIL VERTICAL LADDER


SCALE 1:2

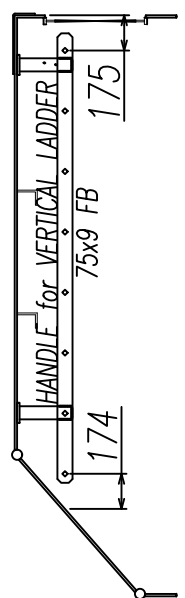

TYP. VERTICAL LADDER TYPE "A"
LOCATION : TANK BELOW MAIN DECK
SIMILAR VLA: 12-11:12

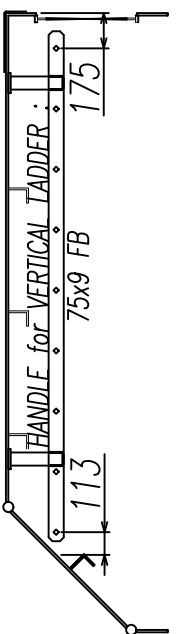

TYP. VERTICAL LADDER TYPE "A"
LOCATION : TANK BELOW MAIN DECK
SIMILAR VLA: 34-56:78&10

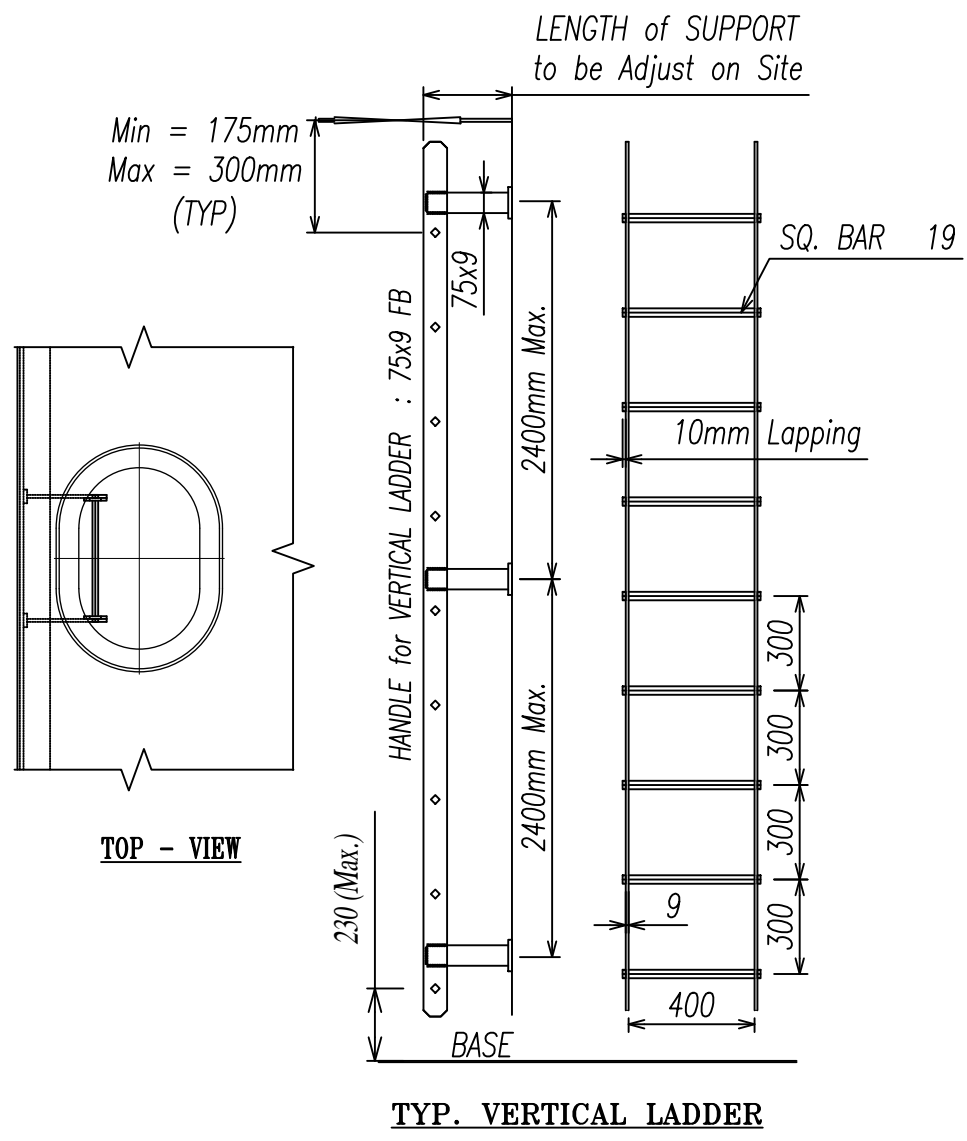

TOP - VIEW

TYP. VERTICAL LADDER

ITEM	MODIFICATION	BY	DATE
OWNER			
BUILDER			
PROJECT			
FLOATING BARGE 144'X50'X10'			
TITLE			
VERTICAL LADDER ARRANGEMENT & DETAIL			
PREPARED	CHECKED	APPROVED	CLASS: BKI
KKH	AR	AR	HULL NO: H560
09/07/2026	09/07/2026	09/07/2026	SHEET: 01 OF 01
SISTER SHIP :-			A1-STD

THIS DOCUMENT AND THE INFORMATION IT CONTAINS IS
COPYRIGHT AND REMAINS THE PROPERTY OF PT BANGSAR ABADI.
THE DESIGN IS NOT TO BE COPIED IN WHOLE OR IN PART OR
DISCLOSED TO ANY THIRD PARTY FOR ANY PURPOSE WITHOUT
PRIOR PERMISSION IN WRITING.