



SECTION AT SIDE SHELL

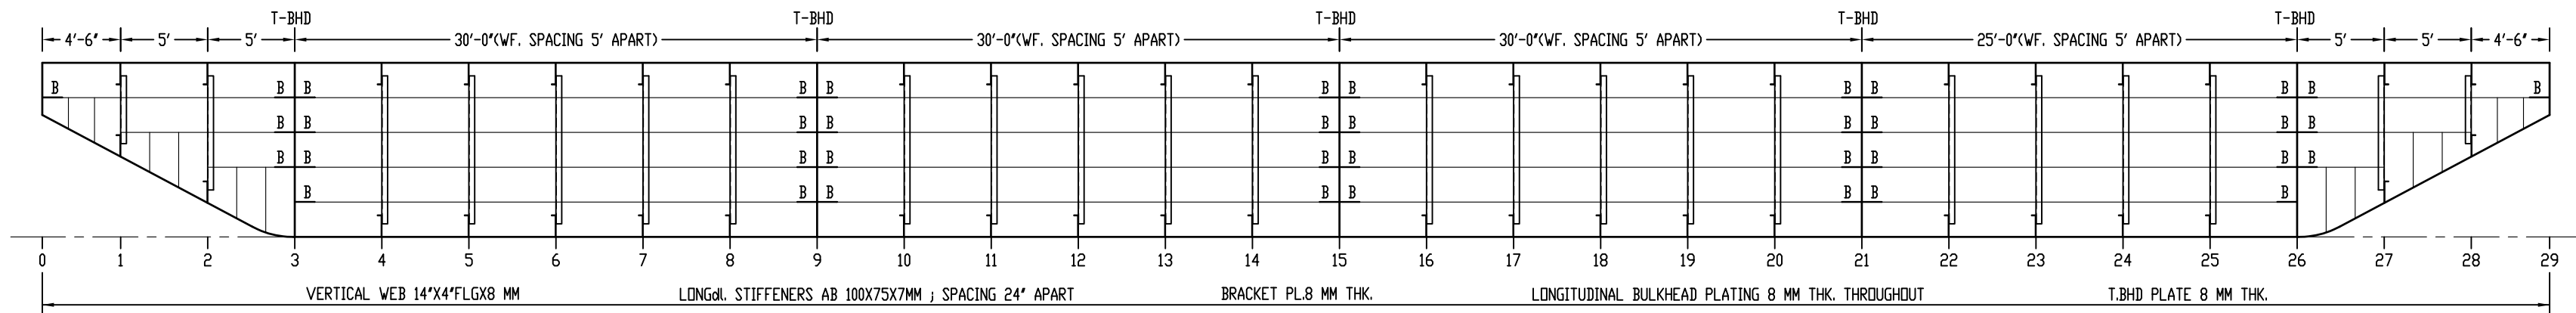


SECTION AT LONGd. BULKHEAD (CENTER LINE)

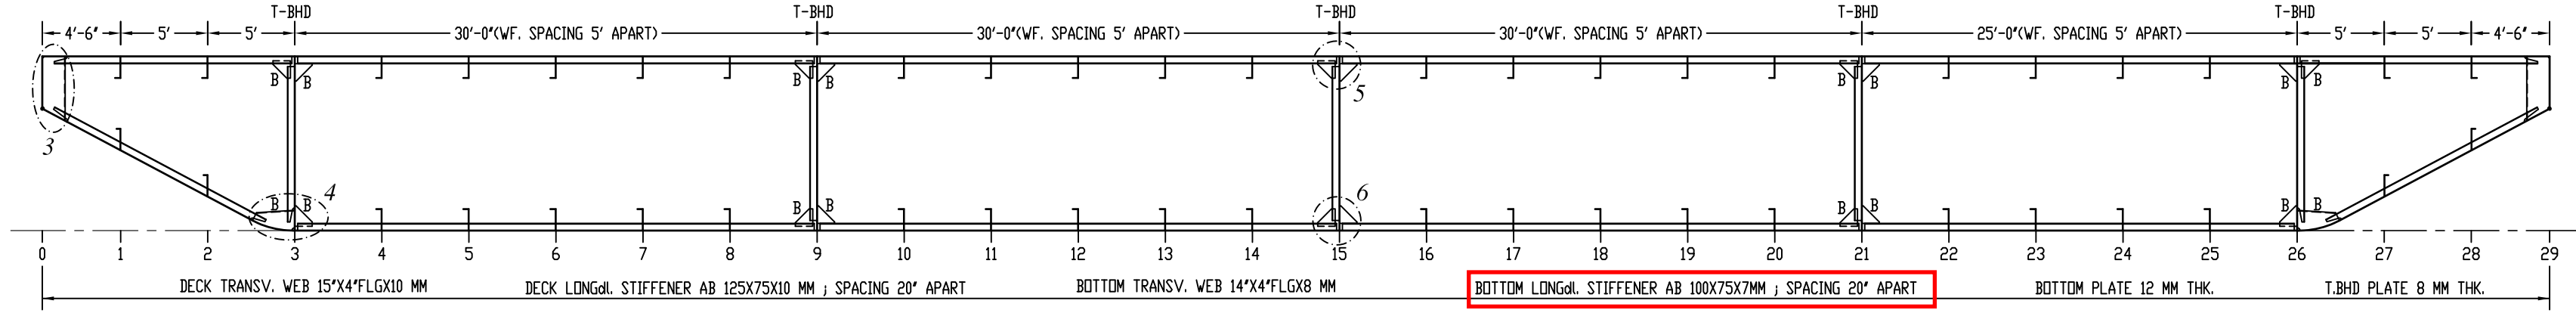


SECTION AT LONGd. STIFFENER

Note : Bottom Longl Stiffener AB 100x75x9MM

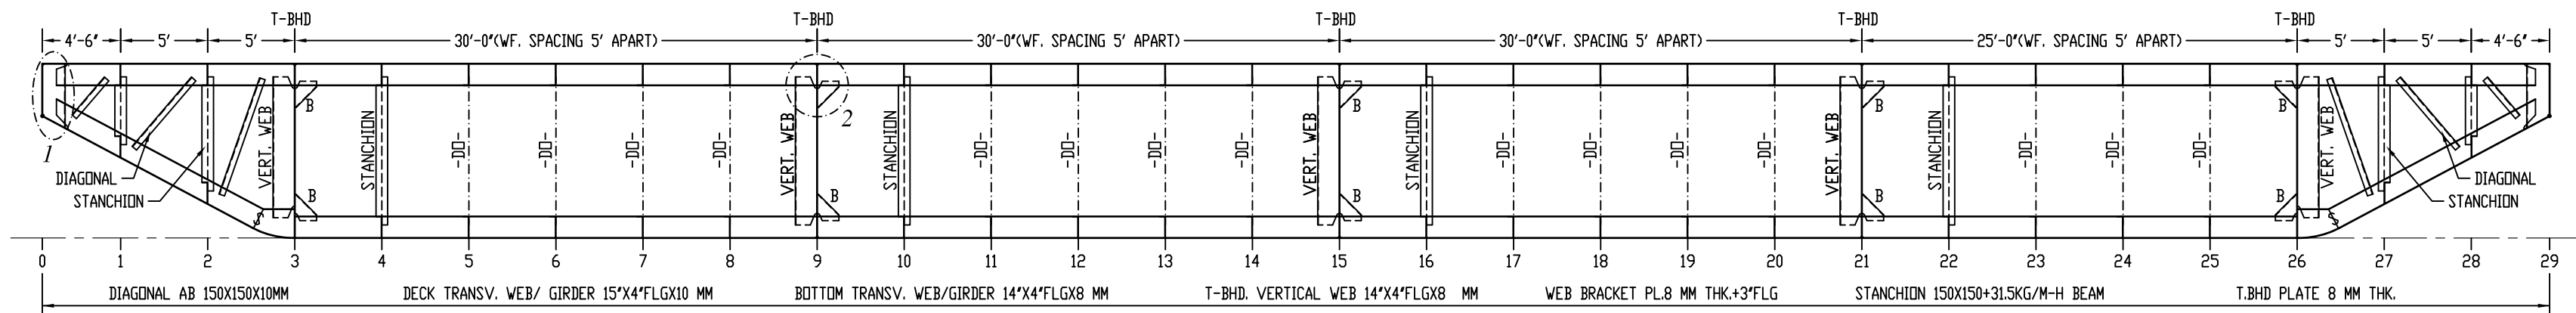


Note : 1. Reinforce main deck on Frame 9-14

2. Plate reinforcement for the mooring bolder installation is not indicated in the drawing.


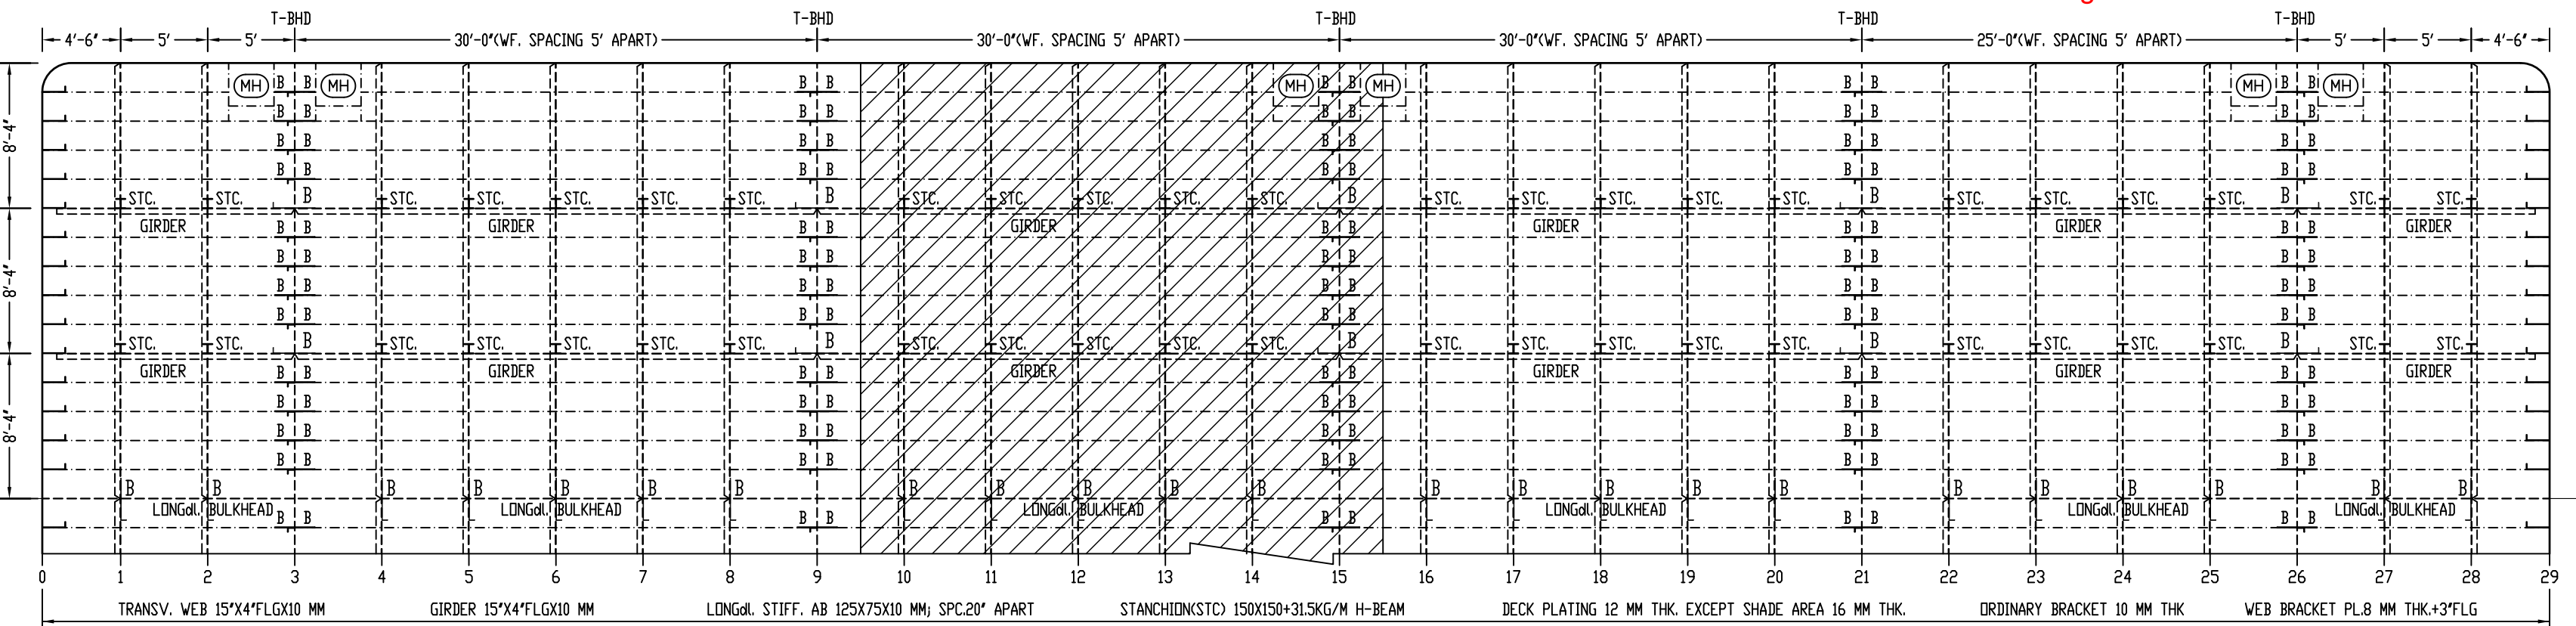


DECK PLAN

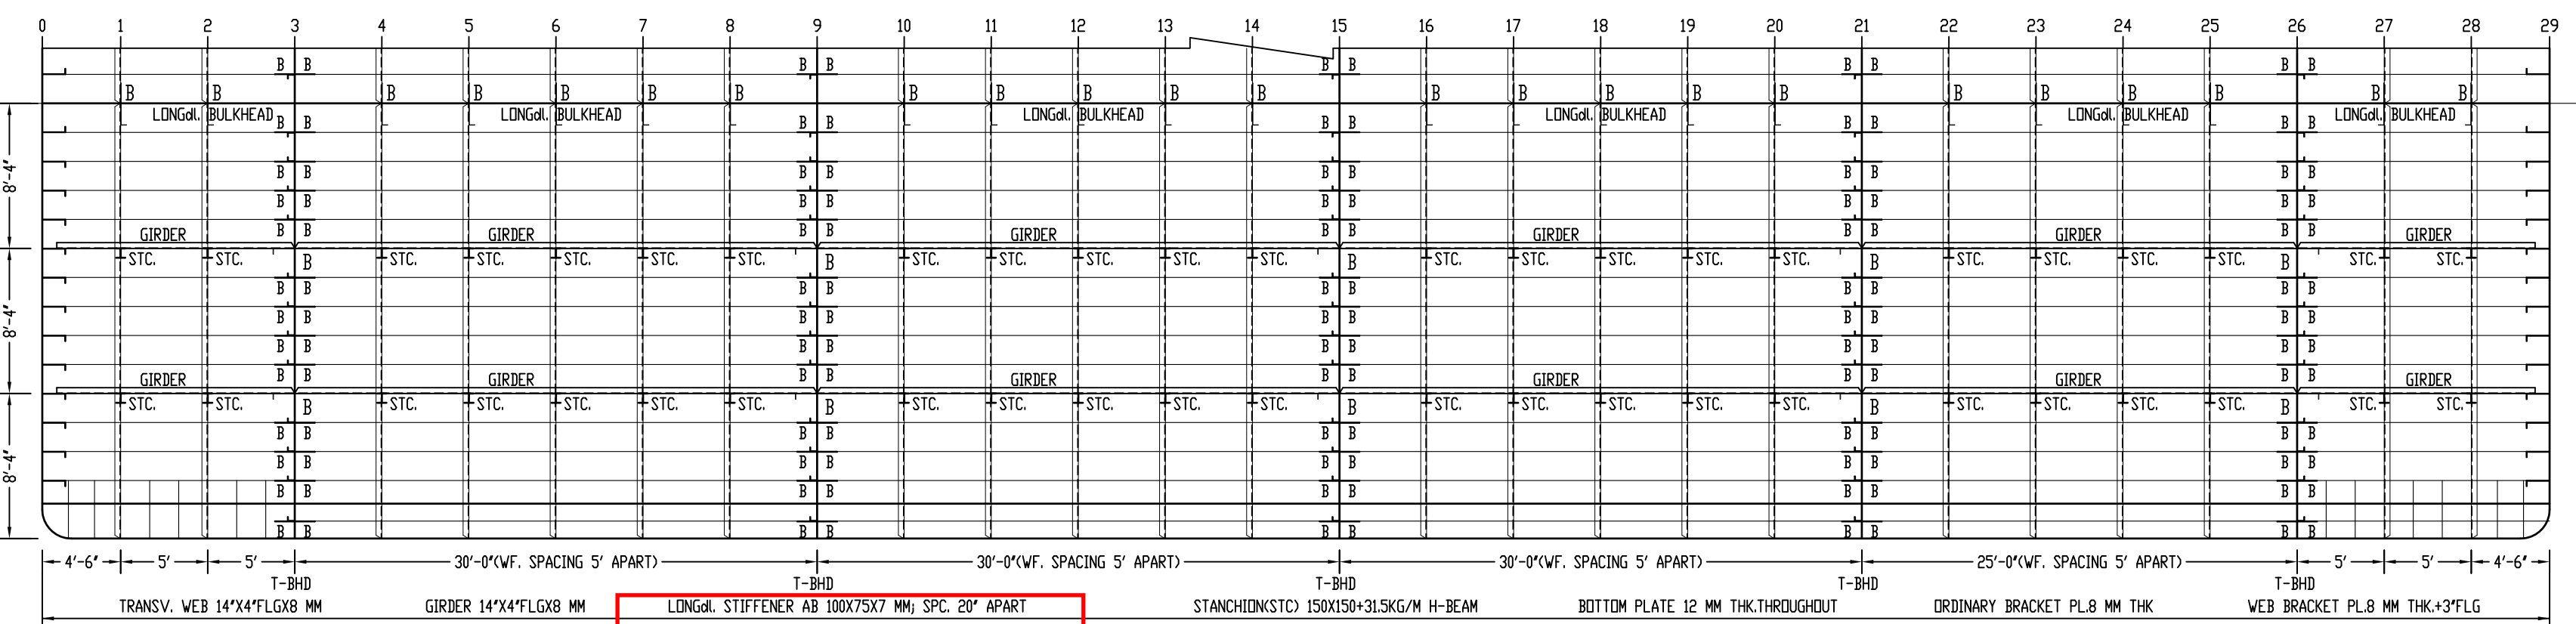


Note : Bottom Longl Stiffener AB 100x75x9MM


BOTTOM PLAN

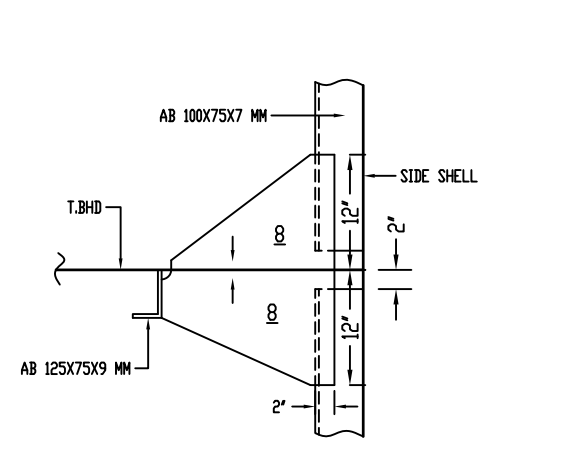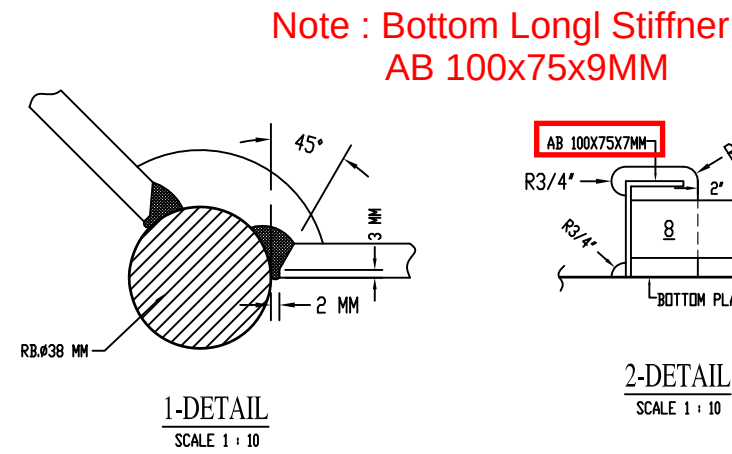


B-B SECTION

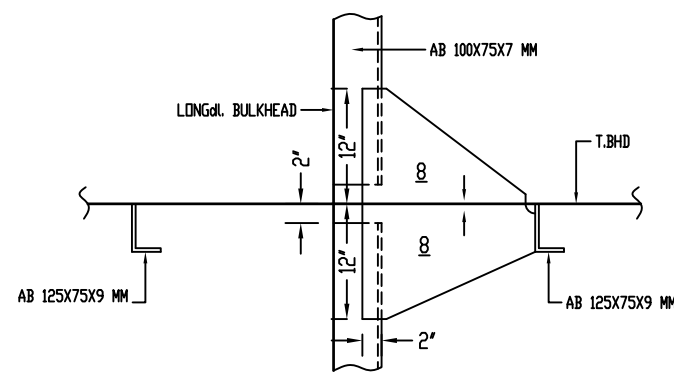

A-A SECTION

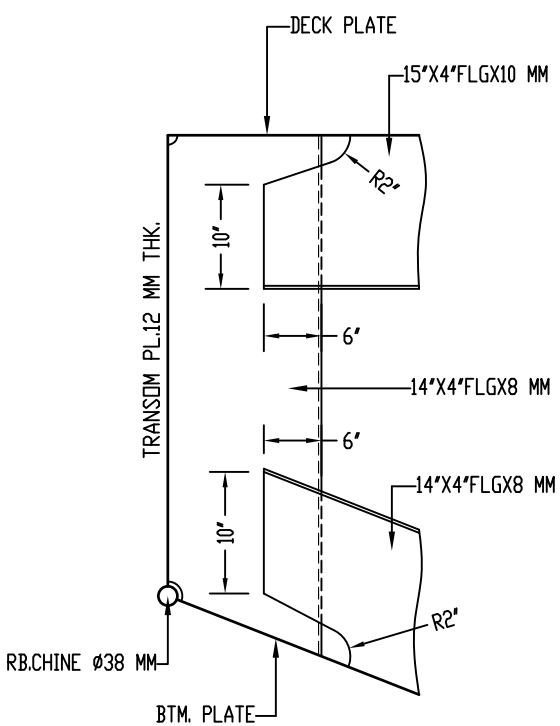


1-DETAIL

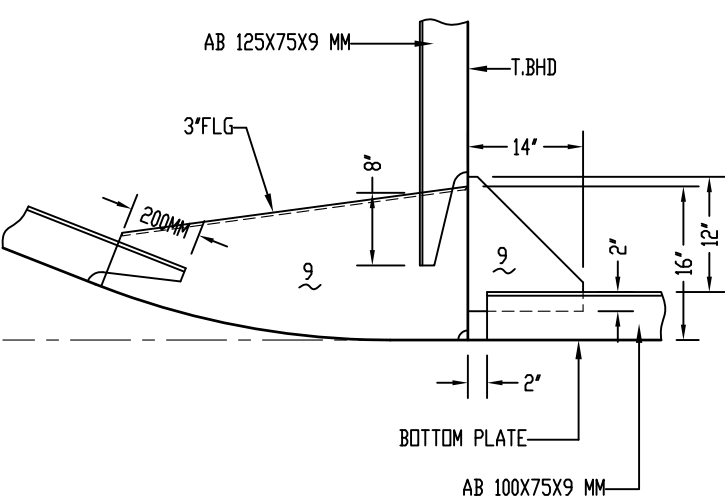


4-DETAIL

MAIN DIMENSIONS :


LENGTH OVER ALL : 144'-0"
BREADTH MOULDED : 50'-0"
DEPTH MOULDED : 10'-0"

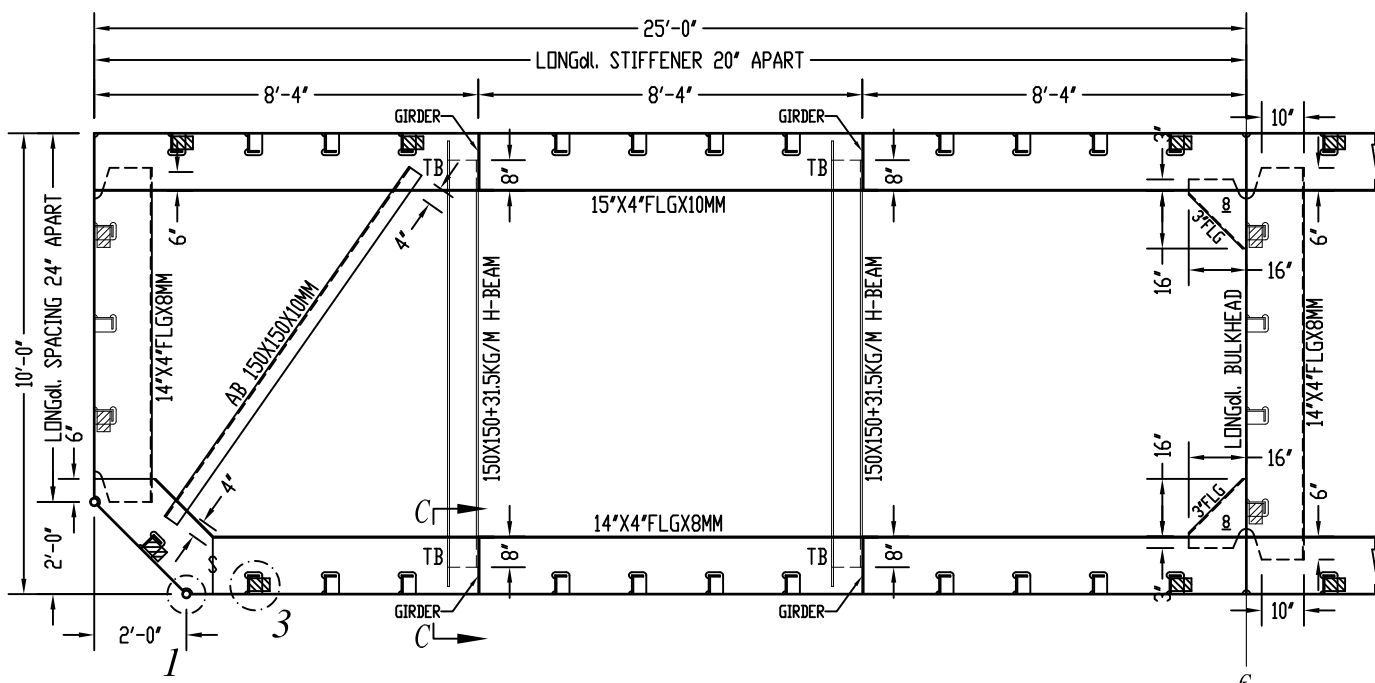


TRANSVERSAL WEB SECTION(TYP)

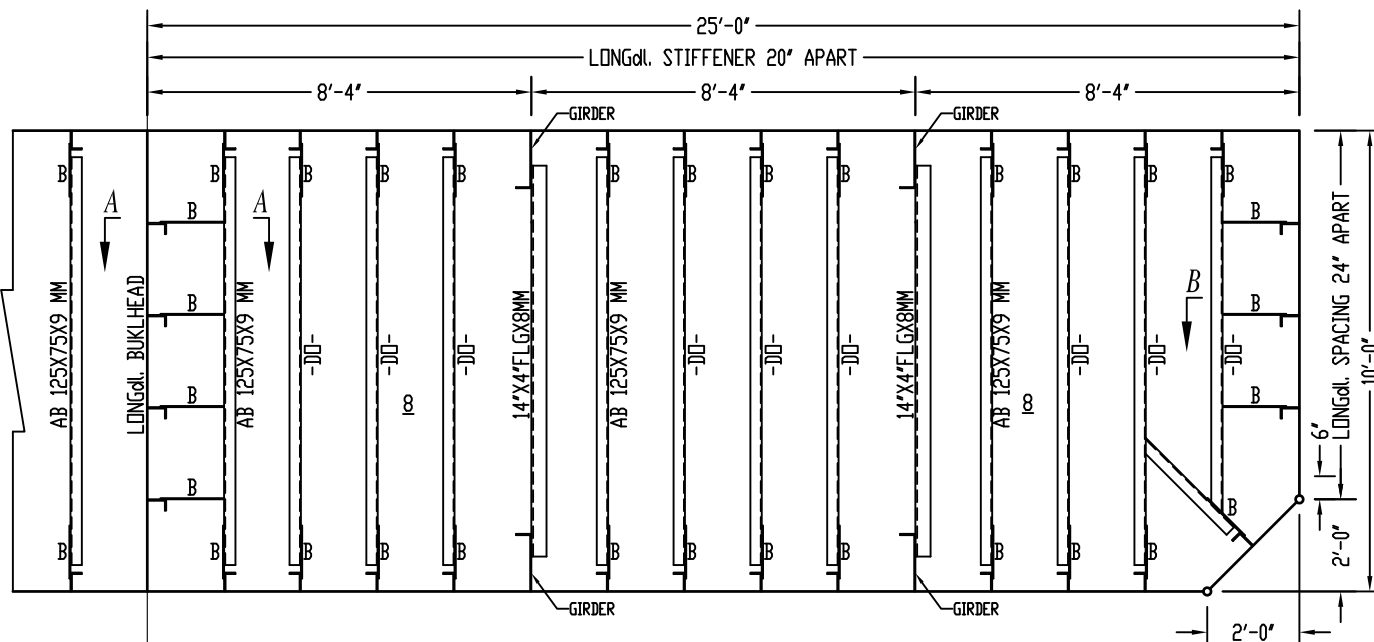


TRANSVERSAL BULKHEAD SECTION(TYP)

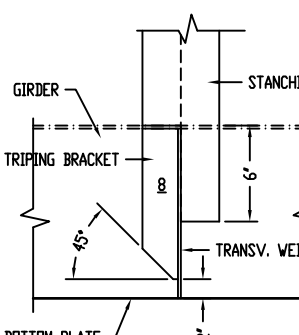


C-C SECTION

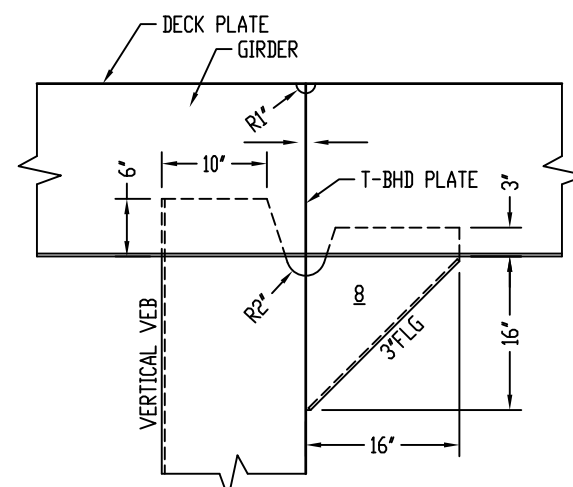


2-DETAIL

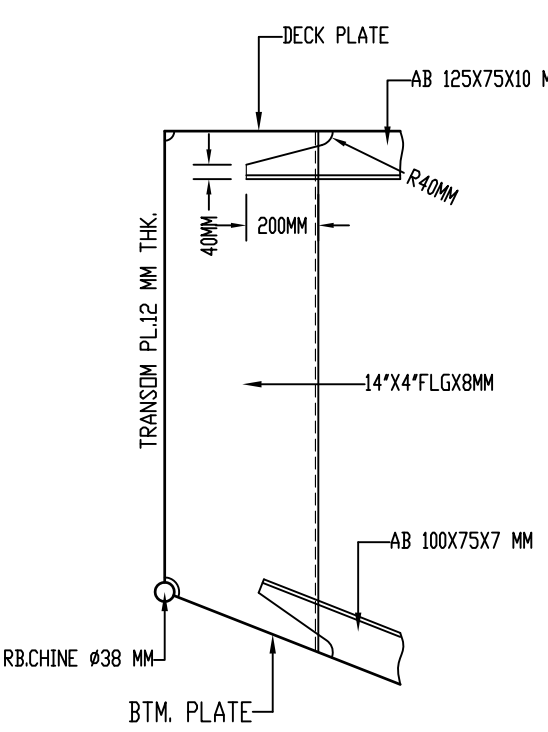


3-DETAIL

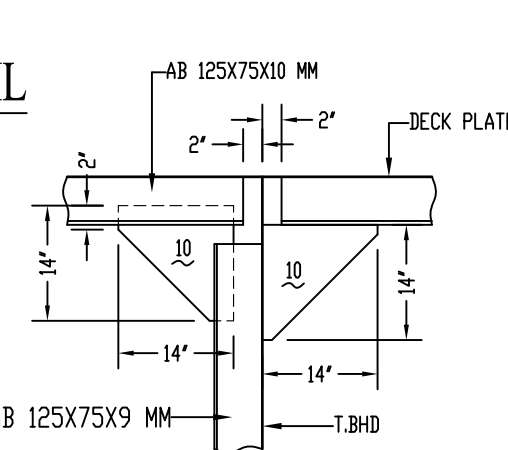

5-DETAIL

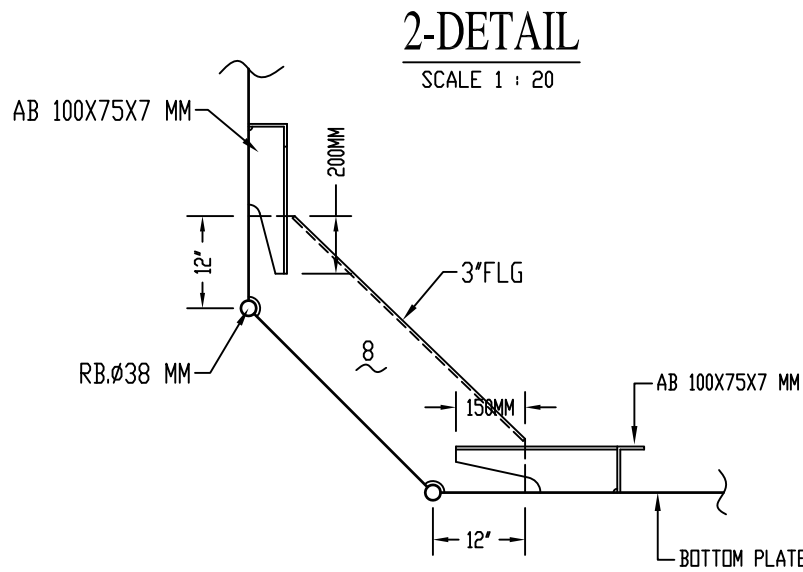

D-D SECTION

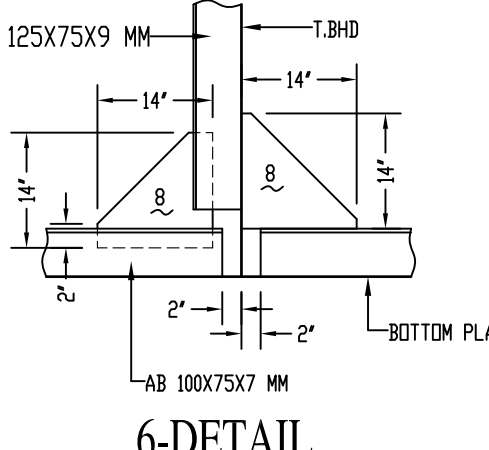

6-DETAIL

ITEM	DETAILS OF MODIFICATION	BY	DATE
BUILDER :			
OWNER :			
PROJECT :	144'X50'X10' DECK CARGO BARGE		
TITLE :	CONSTRUCTION PLAN		
CLASSIFICATION : BKT	HULL NO. :		
DRAWN BY	CHECKED BY	SCALE	DRAWING NUMBER
IND-03	DIK-01	1 : 100	
8 JUNE 2026	8 JUNE 2026		
			REV.
			0