


OUTBOARD PROFILE

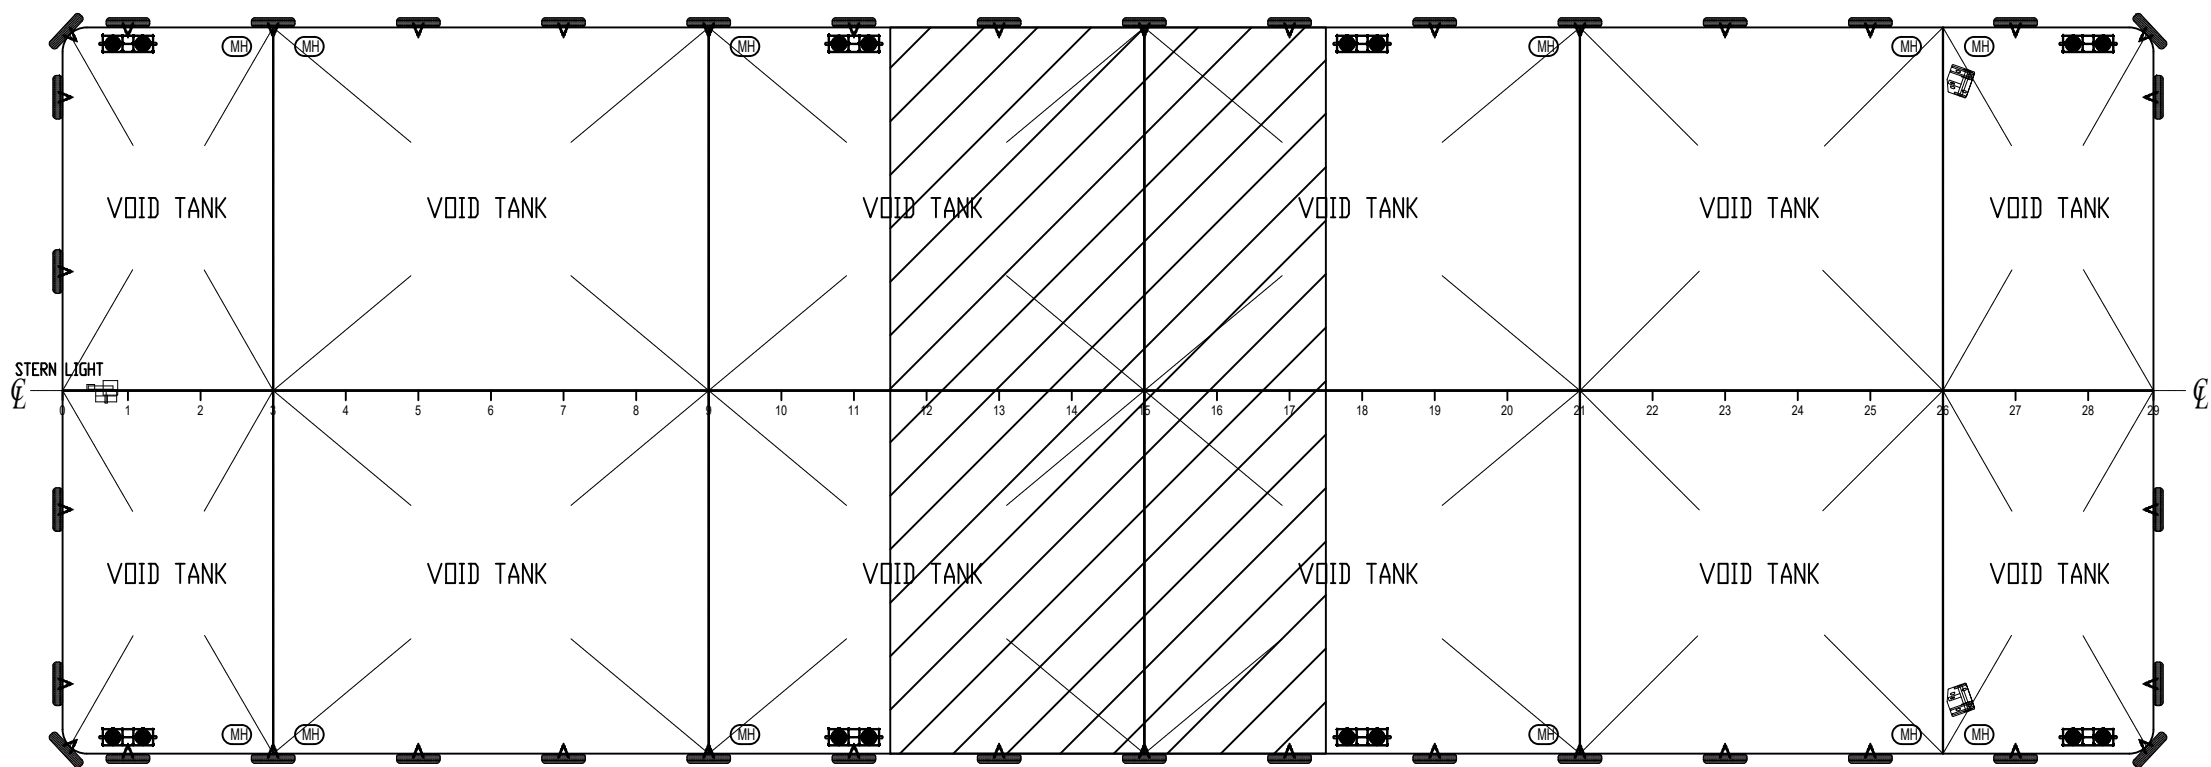

DECK PLAN

MAIN DIMENSIONS :

LENGTH OVER ALL : 144'-0"
BREADTH MOULDED : 50'-0"
DEPTH MOULDED : 10'-0"

THIS DOCUMENT AND THE INFORMATION IT CONTAINS IS
COPYRIGHT AND REMAINS THE PROPERTY OF PT.BANDAR ABADI.
THE DESIGN IS NOT TO BE COPIED IN WHOLE OR IN PART OR
DISCLOSED TO ANY THIRD PARTY FOR ANY PURPOSE WITHOUT
PRIOR PERMISSION IN WRITING.

ITEM	MODIFICATION		BY	DATE
OWNER				
BUILDER				
PROJECT				
<u>FLOATING BARGE</u> 144'x50'x10'				
TITLE				
GENERAL ARRANGEMENT				
PREPARED	CHECKED	APPROVED	CLASS: BKJ	
				SCALE: 1:75
			SHEET: 01 OF 01	REV: 0
SISTER SHIP :-				A1-STD