
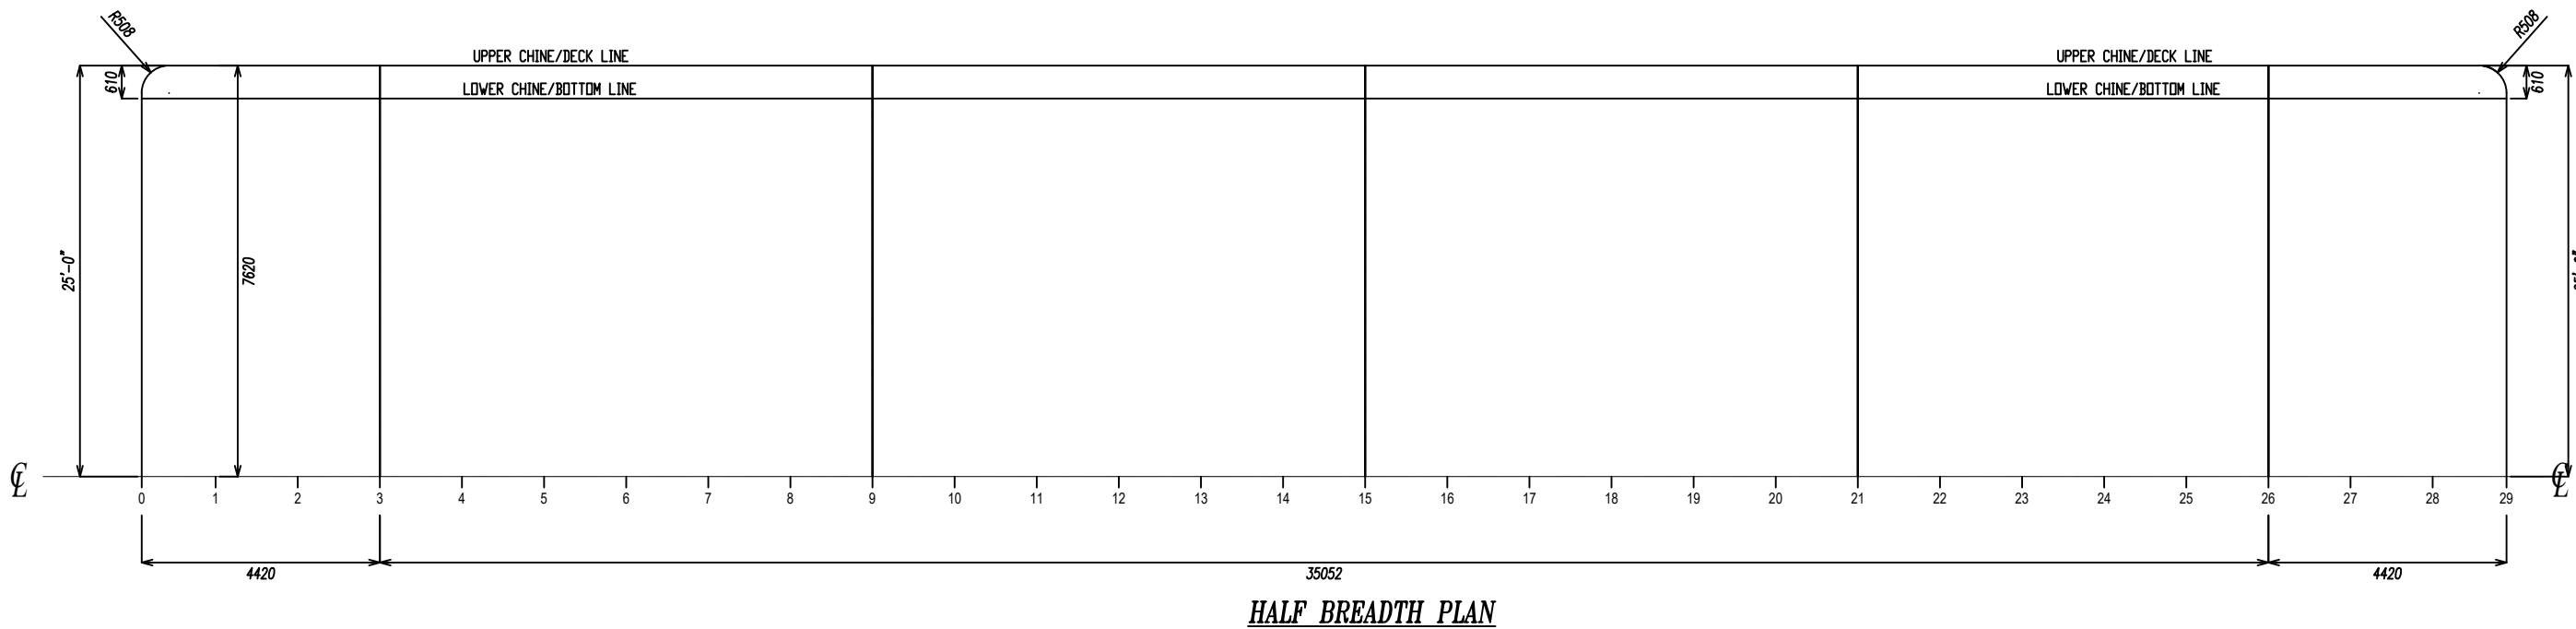


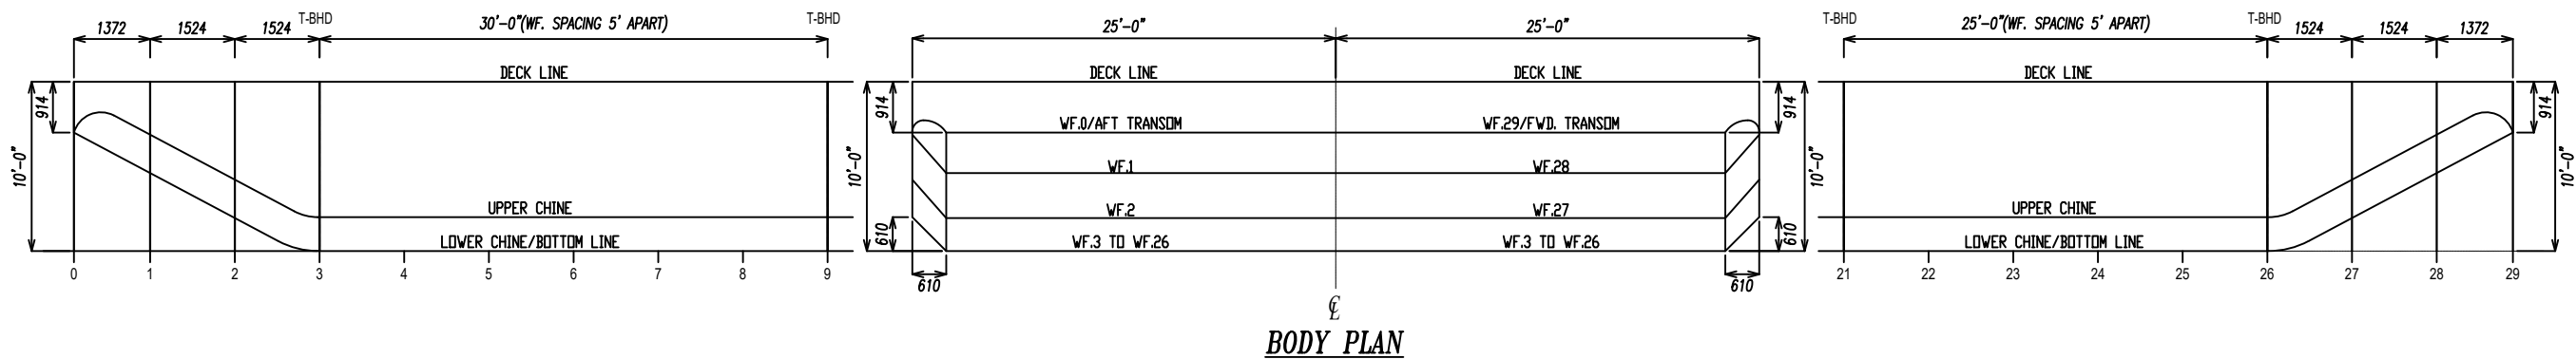

OFFSETS TABLE (MM)

NO. Fr.	HALF BREADTH		HEIGHT ABOVE BASE LINE			NO. Fr.
	LOWER CHINE	UPPER CHINE	LOWER CHINE	UPPER CHINE	DECK LINE	
0	7010	7010	2134	2134	3048	0
1	7010	7620	1404	2095	3048	1
2	7010	7620	594	1285	3048	2
3 - 26	7010	7620	0	610	3048	3 - 26
27	7010	7620	594	1285	3048	27
28	7010	7620	1404	2095	3048	28
29	7010	7010	2134	2134	3048	29

MAIN DIMENSIONS :

LENGTH OVER ALL : 144'-0"
BREADTH MOULDED : 50'-0"
DEPTH MOULDED : 10'-0"

THIS DOCUMENT AND THE INFORMATION IT CONTAINS IS
COPYRIGHT AND REMAINS THE PROPERTY OF PT.BANDAR ABADI.
THE DESIGN IS NOT TO BE COPIED IN WHOLE OR IN PART OR
DISCLOSED TO ANY THIRD PARTY FOR ANY PURPOSE WITHOUT
PRIOR PERMISSION IN WRITING.

	REVISION BASED ON CLASS COMMENTS		KKH	23/07/2026
ITEM	MODIFICATION		BY	DATE
OWNER				
BUILDER				
PROJECT				
FLOATING BRAGE 144'x50'x10'				
TITLE				
LINES PLAN				
PREPARED	CHECKED	APPROVED	CLASS: BK1	
				SCALE: NTS
			SHEET: 01 OF 01	REV : 1
SISTER SHIP : -				A1-STD